

DESPIECE DE VIGA — GRUPO VC1

UNIVERSIDAD NACIONAL DE COLOMBIA
DISEÑO ESTRUCTURAL — GRUPO 6

PROYECTO RESIDENCIAL
SANTA MARTA

VIGA VC1

SECCIÓN 450×550 mm
20 FRAMES


NO EMITIR PARA CONSTRUCCIÓN

Verificación seccional cumple
Falta planta/reanálisis global


Escala: indicadas
Fecha: 17-07-2026
Lámina: 1/2

DESPIECE DE VIGAS

PDF + DXF EDITABLE

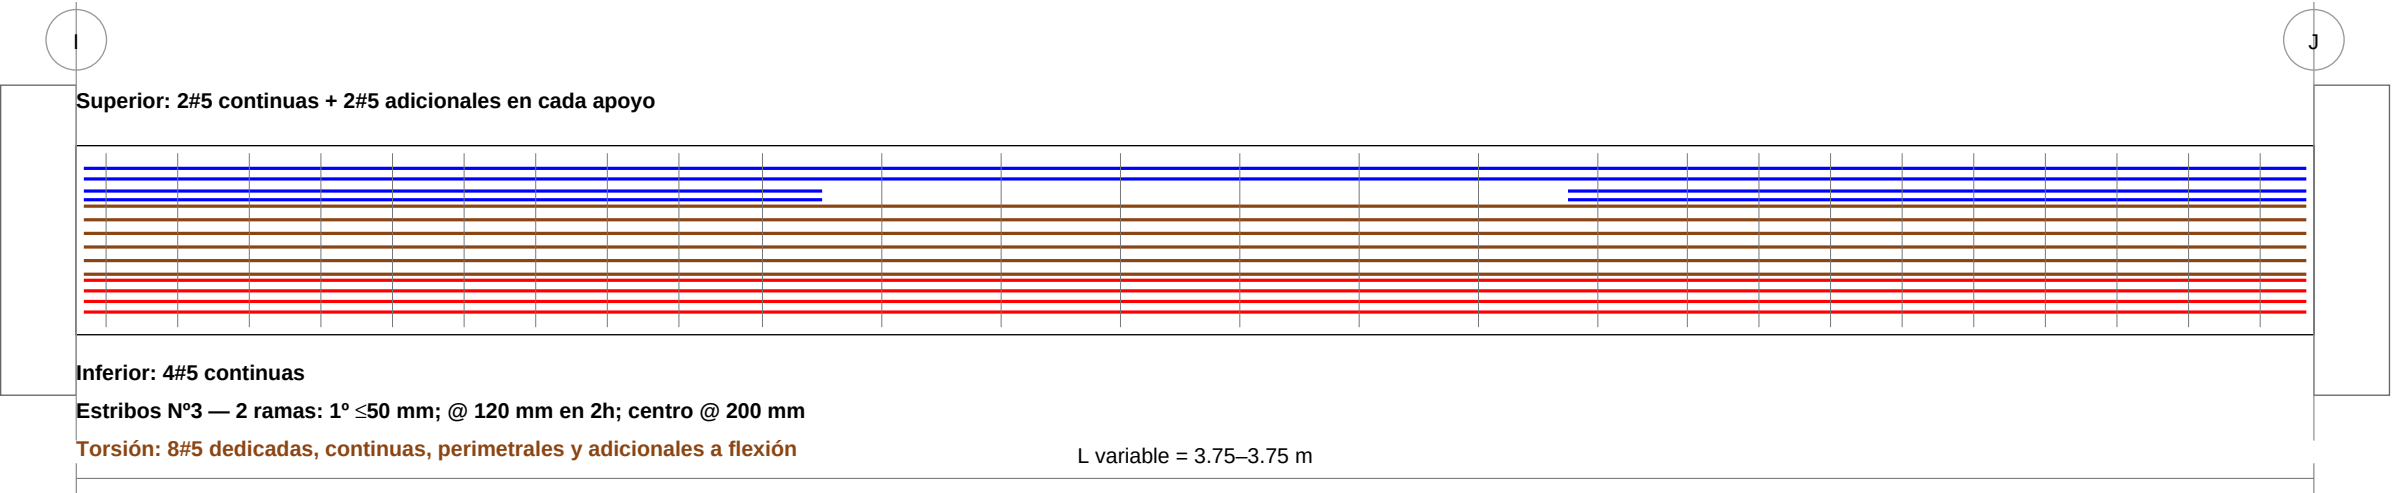


CORTE A-A — APOYO I

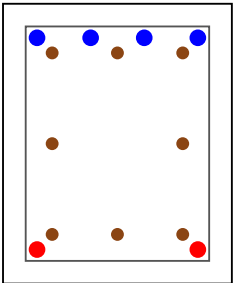


450×550 mm — rec. 40 mm

CORTE B-B — CENTRO

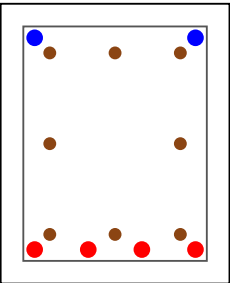

450×550 mm — rec. 40 mm

CORTE C-C — APOYO J

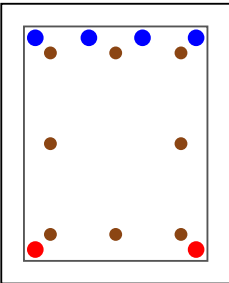

450×550 mm — rec. 40 mm

Nº de vigas: 20 — Frames:
148–149, 153–154, 158–159, 163–164, 168–169, 173–174, 178–179, 183–184, 188–189, 193–194

Mu– máx=33.4 kN·m; Mu+ máx=21.6 kN·m; Vu ENVCORT máx=74.0 kN
Tu diseño bruto=13.2 kN·m; sin reducción automática a ϕTcr ; variantes de longitud: 1
NO EMITIR PARA CONSTRUCCIÓN: detalle académico; usar el cuadro frame–nudos–longitud y completar planta/reanálisis SAP.

Frame	Var.	Joint I	Joint J	L (mm)	Xc	Yc	Zlnivel	#5 sup	#5 inf	#5 tor.	Estribo	s ext/ctr	Estado
148	V1	205	206	3750	5.88	37.70	3.50	4	4	8	Nº3 cerrado 2R	120/200	CUMPLE
149	V1	206	207	3750	9.62	37.70	3.50	4	4	8	Nº3 cerrado 2R	120/200	CUMPLE
153	V1	208	209	3750	5.88	-1.50	3.50	4	4	8	Nº3 cerrado 2R	120/200	CUMPLE
154	V1	209	210	3750	9.62	-1.50	3.50	4	4	8	Nº3 cerrado 2R	120/200	CUMPLE
158	V1	211	212	3750	5.88	-1.50	6.50	4	4	8	Nº3 cerrado 2R	120/200	CUMPLE
159	V1	212	213	3750	9.62	-1.50	6.50	4	4	8	Nº3 cerrado 2R	120/200	CUMPLE
163	V1	214	215	3750	5.88	-1.50	9.50	4	4	0	Nº3 cerrado 2R	120/240	CUMPLE
164	V1	215	216	3750	9.62	-1.50	9.50	4	4	0	Nº3 cerrado 2R	120/240	CUMPLE
168	V1	217	218	3750	5.88	-1.50	12.50	4	4	0	Nº3 cerrado 2R	120/240	CUMPLE
169	V1	218	219	3750	9.62	-1.50	12.50	4	4	0	Nº3 cerrado 2R	120/240	CUMPLE
173	V1	220	221	3750	5.88	-1.50	15.50	4	4	0	Nº3 cerrado 2R	120/240	CUMPLE
174	V1	221	222	3750	9.62	-1.50	15.50	4	4	0	Nº3 cerrado 2R	120/240	CUMPLE
178	V1	223	224	3750	5.88	37.70	6.50	4	4	8	Nº3 cerrado 2R	120/200	CUMPLE
179	V1	224	225	3750	9.62	37.70	6.50	4	4	8	Nº3 cerrado 2R	120/200	CUMPLE
183	V1	226	227	3750	5.88	37.70	9.50	4	4	0	Nº3 cerrado 2R	120/240	CUMPLE
184	V1	227	228	3750	9.62	37.70	9.50	4	4	0	Nº3 cerrado 2R	120/240	CUMPLE
188	V1	229	230	3750	5.88	37.70	12.50	4	4	0	Nº3 cerrado 2R	120/240	CUMPLE
189	V1	230	231	3750	9.62	37.70	12.50	4	4	0	Nº3 cerrado 2R	120/240	CUMPLE
193	V1	232	233	3750	5.88	37.70	15.50	4	4	0	Nº3 cerrado 2R	120/240	CUMPLE
194	V1	233	234	3750	9.62	37.70	15.50	4	4	0	Nº3 cerrado 2R	120/240	CUMPLE