

DESPIECE DE VIGA — GRUPO VC4

UNIVERSIDAD NACIONAL DE COLOMBIA
DISEÑO ESTRUCTURAL — GRUPO 6

PROYECTO RESIDENCIAL
SANTA MARTA


VIGA VC4

SECCIÓN 450×550 mm
20 FRAMES


NO EMITIR PARA CONSTRUCCIÓN
4 frames NO CUMPLEN
61, 62, 87, 88

Escala: indicadas
Fecha: 17-07-2026
Lámina: 1/2

DESPIECE DE VIGAS
PDF + DXF EDITABLE

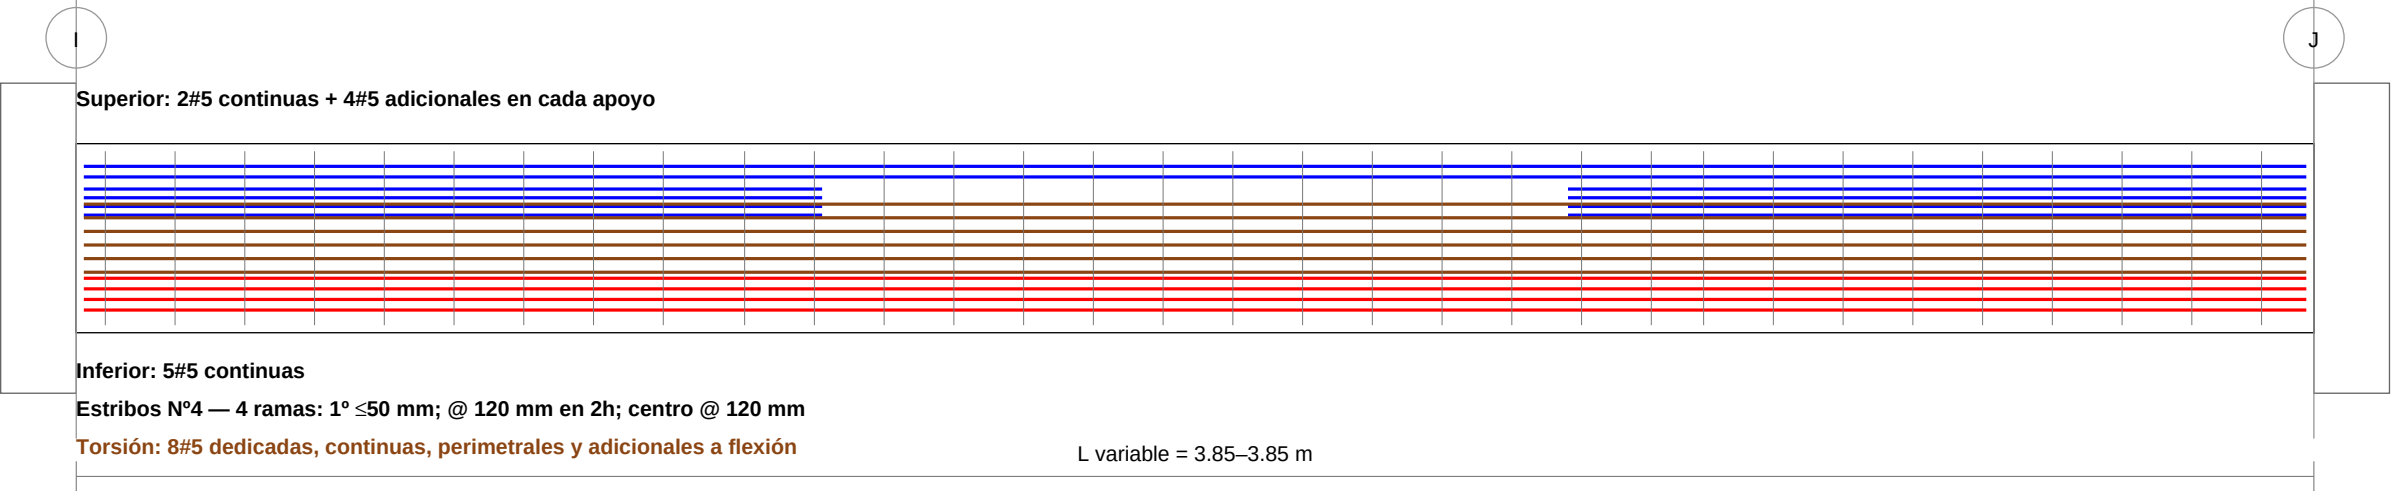


CORTE A-A — APOYO I

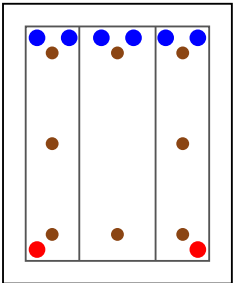


450×550 mm — rec. 40 mm

CORTE B-B — CENTRO

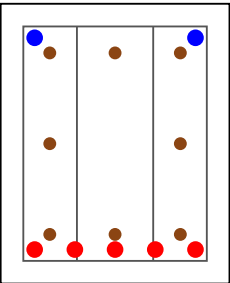

450×550 mm — rec. 40 mm

CORTE C-C — APOYO J

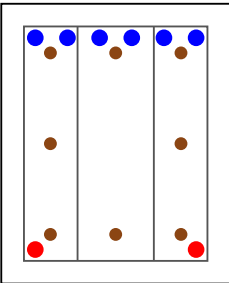

450×550 mm — rec. 40 mm

Nº de vigas: 20 — Frames:
61–62, 87–88, 261–262, 287–288, 819–820, 845–846, 913–914, 939–940, 1007–1008, 1033–1034

Mu– máx=205.0 kN·m; Mu+ máx=173.6 kN·m; Vu ENVCORT máx=506.8 kN
Tu diseño bruto=74.8 kN·m; sin reducción automática a ϕTcr ; variantes de longitud: 1
NO EMITIR PARA CONSTRUCCIÓN: detalle académico; usar el cuadro frame–nudos–longitud y completar planta/reanálisis SAP.

Frame	Var.	Joint I	Joint J	L (mm)	Xc	Yc	Z/nivel	#5 sup	#5 inf	#5 tor.	Estribo	s ext/ctr	Estado
61	V1	3	23	3850	1.93	6.25	3.50	6	5	8	Nº4 cerrado 4R	120/120	NO CUMPLE V-T
62	V1	47	52	3850	13.57	6.25	3.50	6	5	8	Nº4 cerrado 4R	120/120	NO CUMPLE V-T
87	V1	10	15	3850	1.93	29.95	3.50	6	5	8	Nº4 cerrado 4R	120/120	NO CUMPLE V-T
88	V1	39	59	3850	13.57	29.95	3.50	6	5	8	Nº4 cerrado 4R	120/120	NO CUMPLE V-T
261	V1	129	149	3850	1.93	6.25	6.50	5	5	8	Nº3 cerrado 4R	80/80	CUMPLE
262	V1	173	178	3850	13.57	6.25	6.50	6	5	8	Nº3 cerrado 4R	80/80	CUMPLE
287	V1	136	141	3850	1.93	29.95	6.50	5	5	8	Nº3 cerrado 4R	80/80	CUMPLE
288	V1	165	185	3850	13.57	29.95	6.50	6	5	8	Nº3 cerrado 4R	80/80	CUMPLE
819	V1	493	513	3850	1.93	6.25	9.50	4	4	8	Nº4 cerrado 2R	110/110	CUMPLE
820	V1	537	542	3850	13.57	6.25	9.50	4	4	8	Nº4 cerrado 2R	110/110	CUMPLE
845	V1	500	505	3850	1.93	29.95	9.50	4	4	8	Nº4 cerrado 2R	110/110	CUMPLE
846	V1	529	549	3850	13.57	29.95	9.50	4	4	8	Nº4 cerrado 2R	110/110	CUMPLE
913	V1	554	574	3850	1.93	6.25	12.50	4	4	8	Nº3 cerrado 2R	120/130	CUMPLE
914	V1	598	603	3850	13.57	6.25	12.50	4	4	8	Nº3 cerrado 2R	120/130	CUMPLE
939	V1	561	566	3850	1.93	29.95	12.50	4	4	8	Nº3 cerrado 2R	120/130	CUMPLE
940	V1	590	610	3850	13.57	29.95	12.50	4	4	8	Nº3 cerrado 2R	120/130	CUMPLE
1007	V1	615	635	3850	1.93	6.25	15.50	4	4	0	Nº3 cerrado 2R	120/240	CUMPLE
1008	V1	659	664	3850	13.57	6.25	15.50	4	4	0	Nº3 cerrado 2R	120/240	CUMPLE
1033	V1	622	627	3850	1.93	29.95	15.50	4	4	0	Nº3 cerrado 2R	120/240	CUMPLE
1034	V1	651	671	3850	13.57	29.95	15.50	4	4	0	Nº3 cerrado 2R	120/240	CUMPLE