



DESPIECE DE VIGA — GRUPO VR N1

UNIVERSIDAD NACIONAL DE COLOMBIA DISEÑO ESTRUCTURAL — GRUPO 6
PROYECTO RESIDENCIAL SANTA MARTA
VIGA VR N1
SECCIÓN 500×550 mm 22 FRAMES
NO EMITIR PARA CONSTRUCCIÓN Verificación seccional cumple Falta planta/reanálisis global
Escala: indicadas Fecha: 17-07-2026 Lámina: 1/2
DESPIECE DE VIGAS PDF + DXF EDITABLE

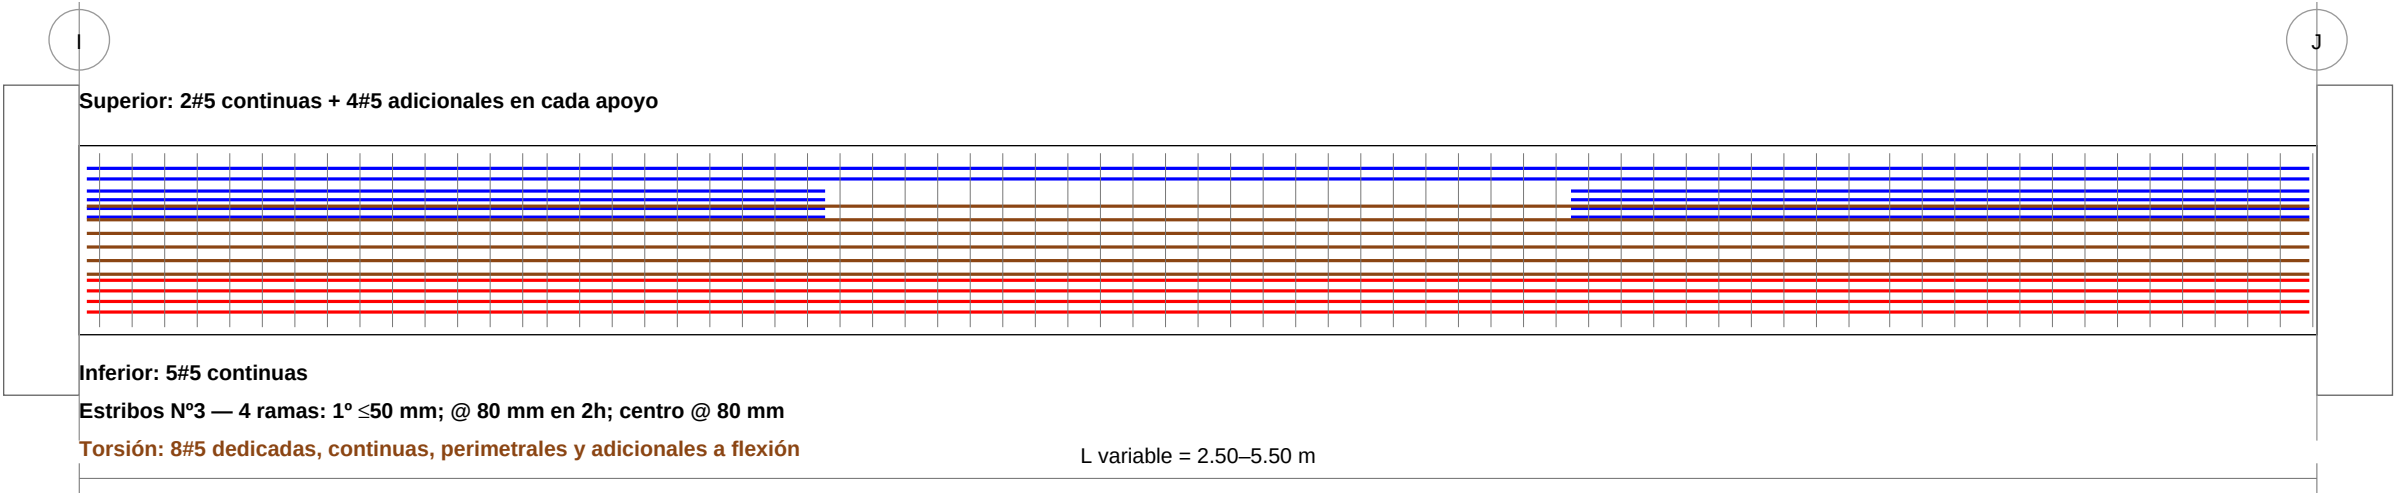


CORTE A-A — APOYO I

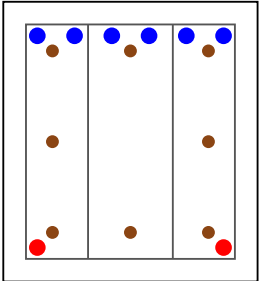


500×550 mm — rec. 40 mm

CORTE B-B — CENTRO

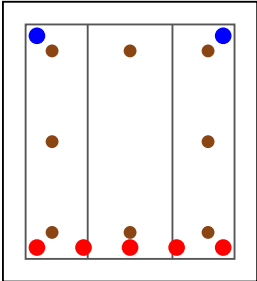

500×550 mm — rec. 40 mm

CORTE C-C — APOYO J

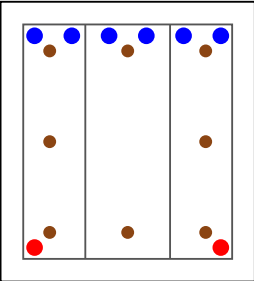

500×550 mm — rec. 40 mm

Nº de vigas: 22 — Frames:

1–10, 45–54, 99–100

Mu– máx=203.7 kN·m; Mu+ máx=164.9 kN·m; Vu ENVCORT máx=703.3 kN

Tu diseño bruto=15.1 kN·m; sin reducción automática a ϕTcr ; variantes de longitud: 5

NO EMITIR PARA CONSTRUCCIÓN: detalle académico; usar el cuadro frame–nudos–longitud y completar planta/reanálisis SAP.

Frame	Var.	Joint I	Joint J	L (mm)	Xc	Yc	Z/nivel	#5 sup	#5 inf	#5 tor.	Estribo	s ext/ctr	Estado
1	V2	1	2	2600	0.00	1.30	3.50	6	5	0	Nº3 cerrado 4R	80/80	CUMPLE
2	V3	2	3	3650	0.00	4.42	3.50	6	5	0	Nº4 cerrado 2R	120/140	CUMPLE
3	V2	3	4	2600	0.00	7.55	3.50	5	5	0	Nº4 cerrado 2R	80/80	CUMPLE
4	V1	4	5	2500	0.00	10.10	3.50	6	5	0	Nº3 cerrado 4R	80/80	CUMPLE
5	V4	5	6	4000	0.00	13.35	3.50	6	5	8	Nº4 cerrado 2R	120/140	CUMPLE
6	V4	7	8	4000	0.00	22.85	3.50	6	5	8	Nº4 cerrado 2R	120/140	CUMPLE
7	V1	8	9	2500	0.00	26.10	3.50	6	5	0	Nº3 cerrado 4R	80/80	CUMPLE
8	V2	9	10	2600	0.00	28.65	3.50	5	5	0	Nº4 cerrado 2R	80/80	CUMPLE
9	V3	10	11	3650	0.00	31.77	3.50	6	5	0	Nº4 cerrado 2R	120/140	CUMPLE
10	V2	11	12	2600	0.00	34.90	3.50	6	5	0	Nº3 cerrado 4R	80/80	CUMPLE
45	V2	50	51	2600	15.50	1.30	3.50	6	5	0	Nº3 cerrado 4R	80/80	CUMPLE
46	V3	51	52	3650	15.50	4.42	3.50	6	5	0	Nº4 cerrado 2R	120/140	CUMPLE
47	V2	52	53	2600	15.50	7.55	3.50	5	5	0	Nº4 cerrado 2R	80/80	CUMPLE
48	V1	53	54	2500	15.50	10.10	3.50	6	5	0	Nº3 cerrado 4R	80/80	CUMPLE
49	V4	54	55	4000	15.50	13.35	3.50	6	5	8	Nº4 cerrado 2R	120/140	CUMPLE
50	V4	56	57	4000	15.50	22.85	3.50	6	5	8	Nº4 cerrado 2R	120/140	CUMPLE
51	V1	57	58	2500	15.50	26.10	3.50	6	5	0	Nº3 cerrado 4R	80/80	CUMPLE
52	V2	58	59	2600	15.50	28.65	3.50	5	5	0	Nº4 cerrado 2R	80/80	CUMPLE
53	V3	59	60	3650	15.50	31.77	3.50	6	5	0	Nº4 cerrado 2R	120/140	CUMPLE
54	V2	60	61	2600	15.50	34.90	3.50	6	5	0	Nº3 cerrado 4R	80/80	CUMPLE
99	V5	7	6	5500	0.00	18.10	3.50	6	5	0	Nº3 cerrado 2R	120/200	CUMPLE
100	V5	56	55	5500	15.50	18.10	3.50	6	5	0	Nº3 cerrado 2R	120/200	CUMPLE