


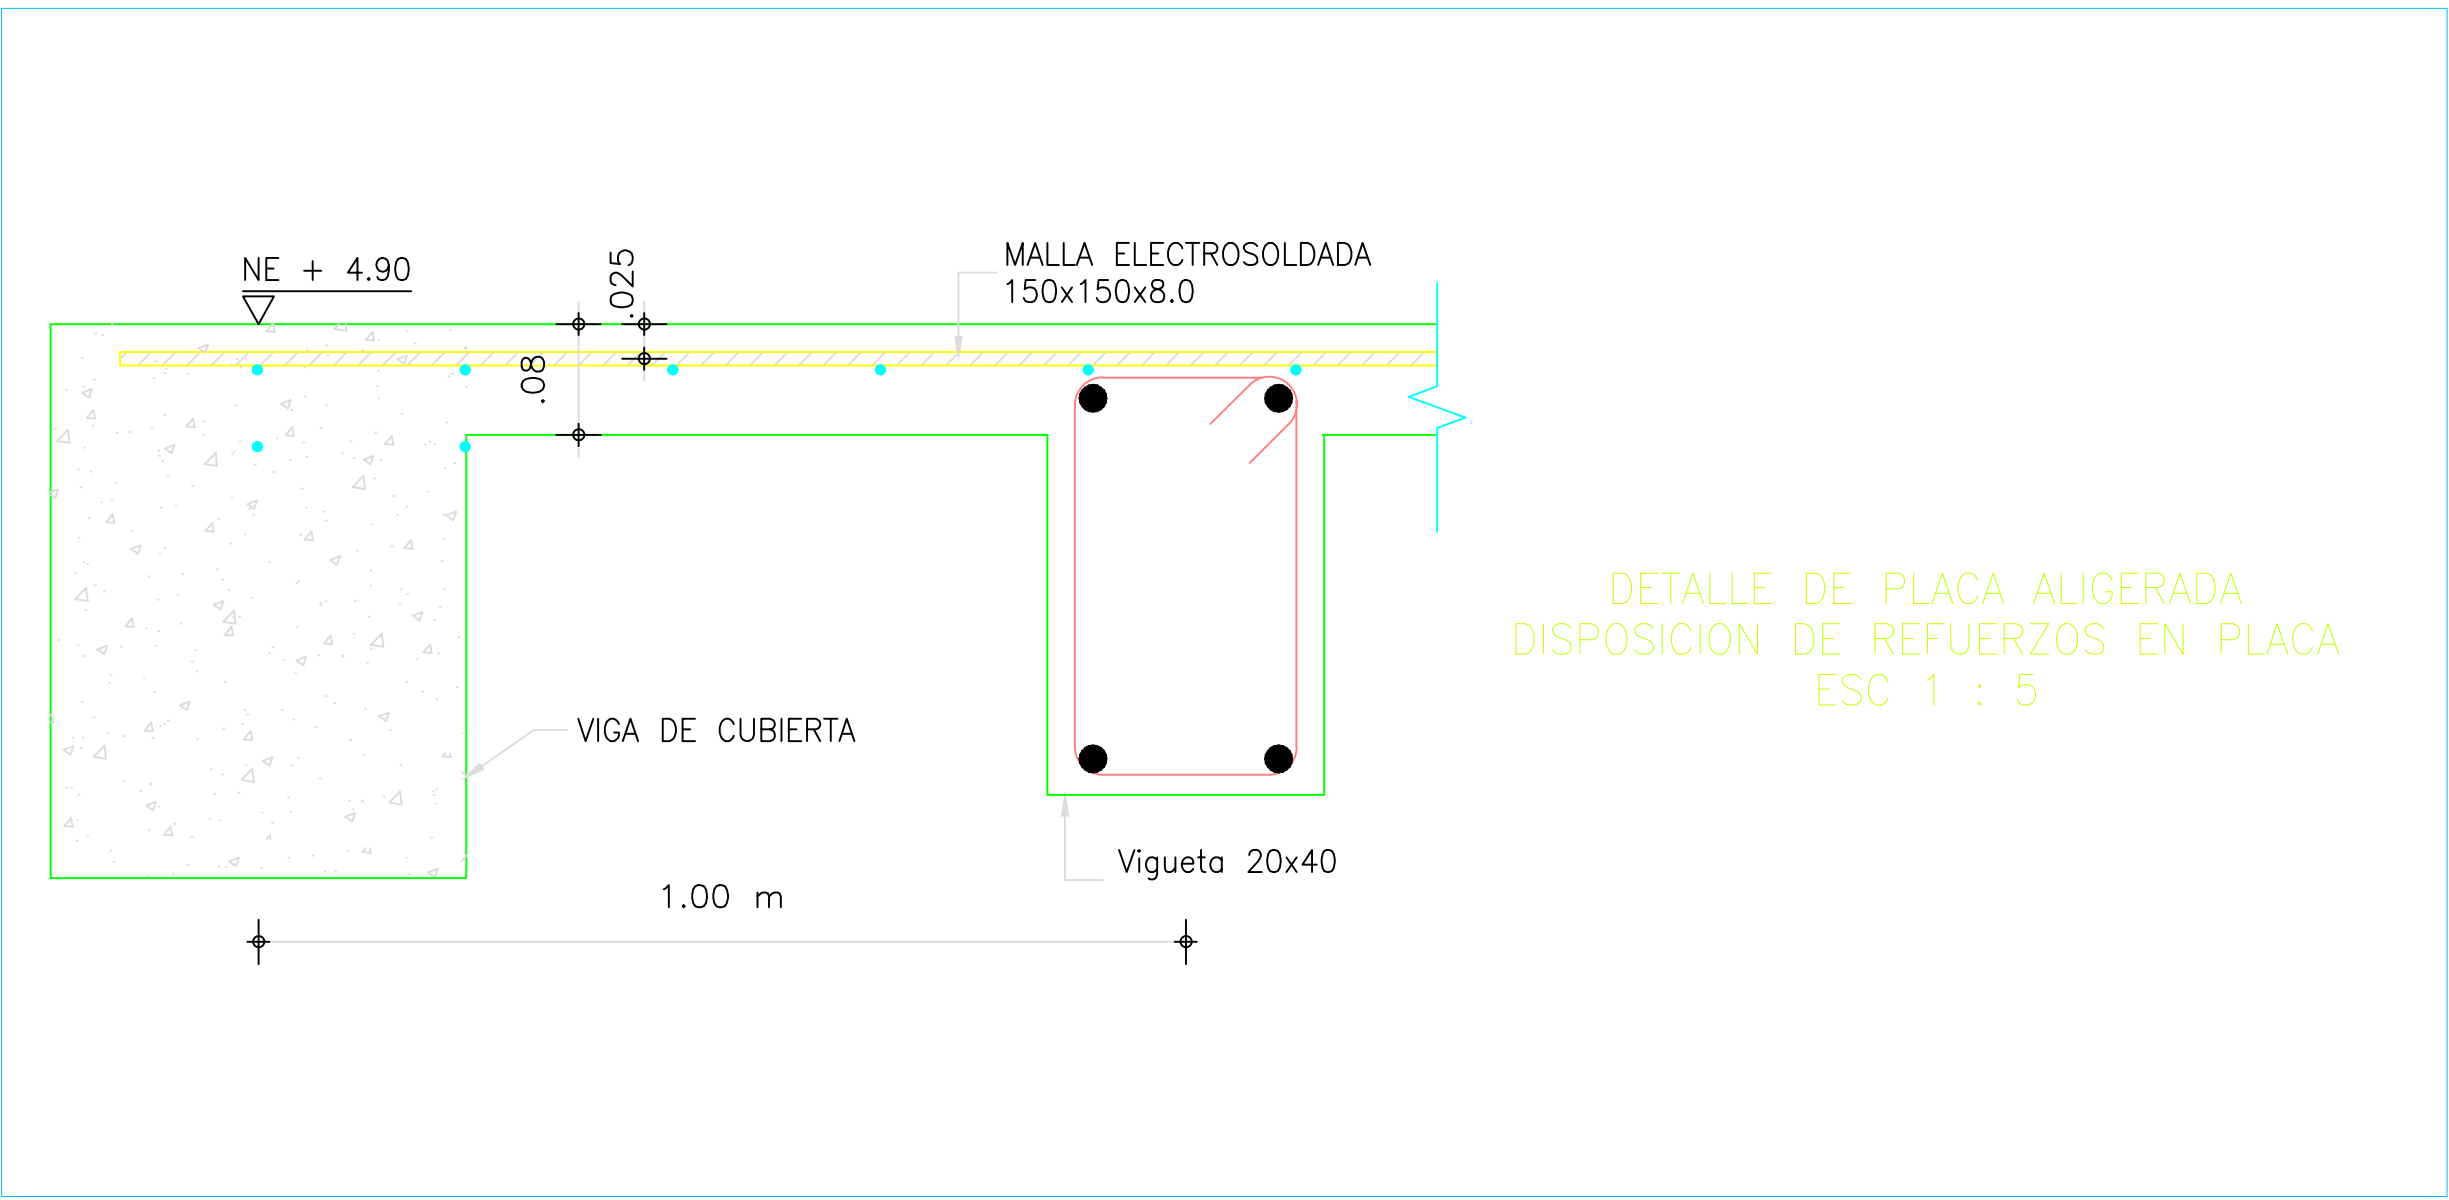
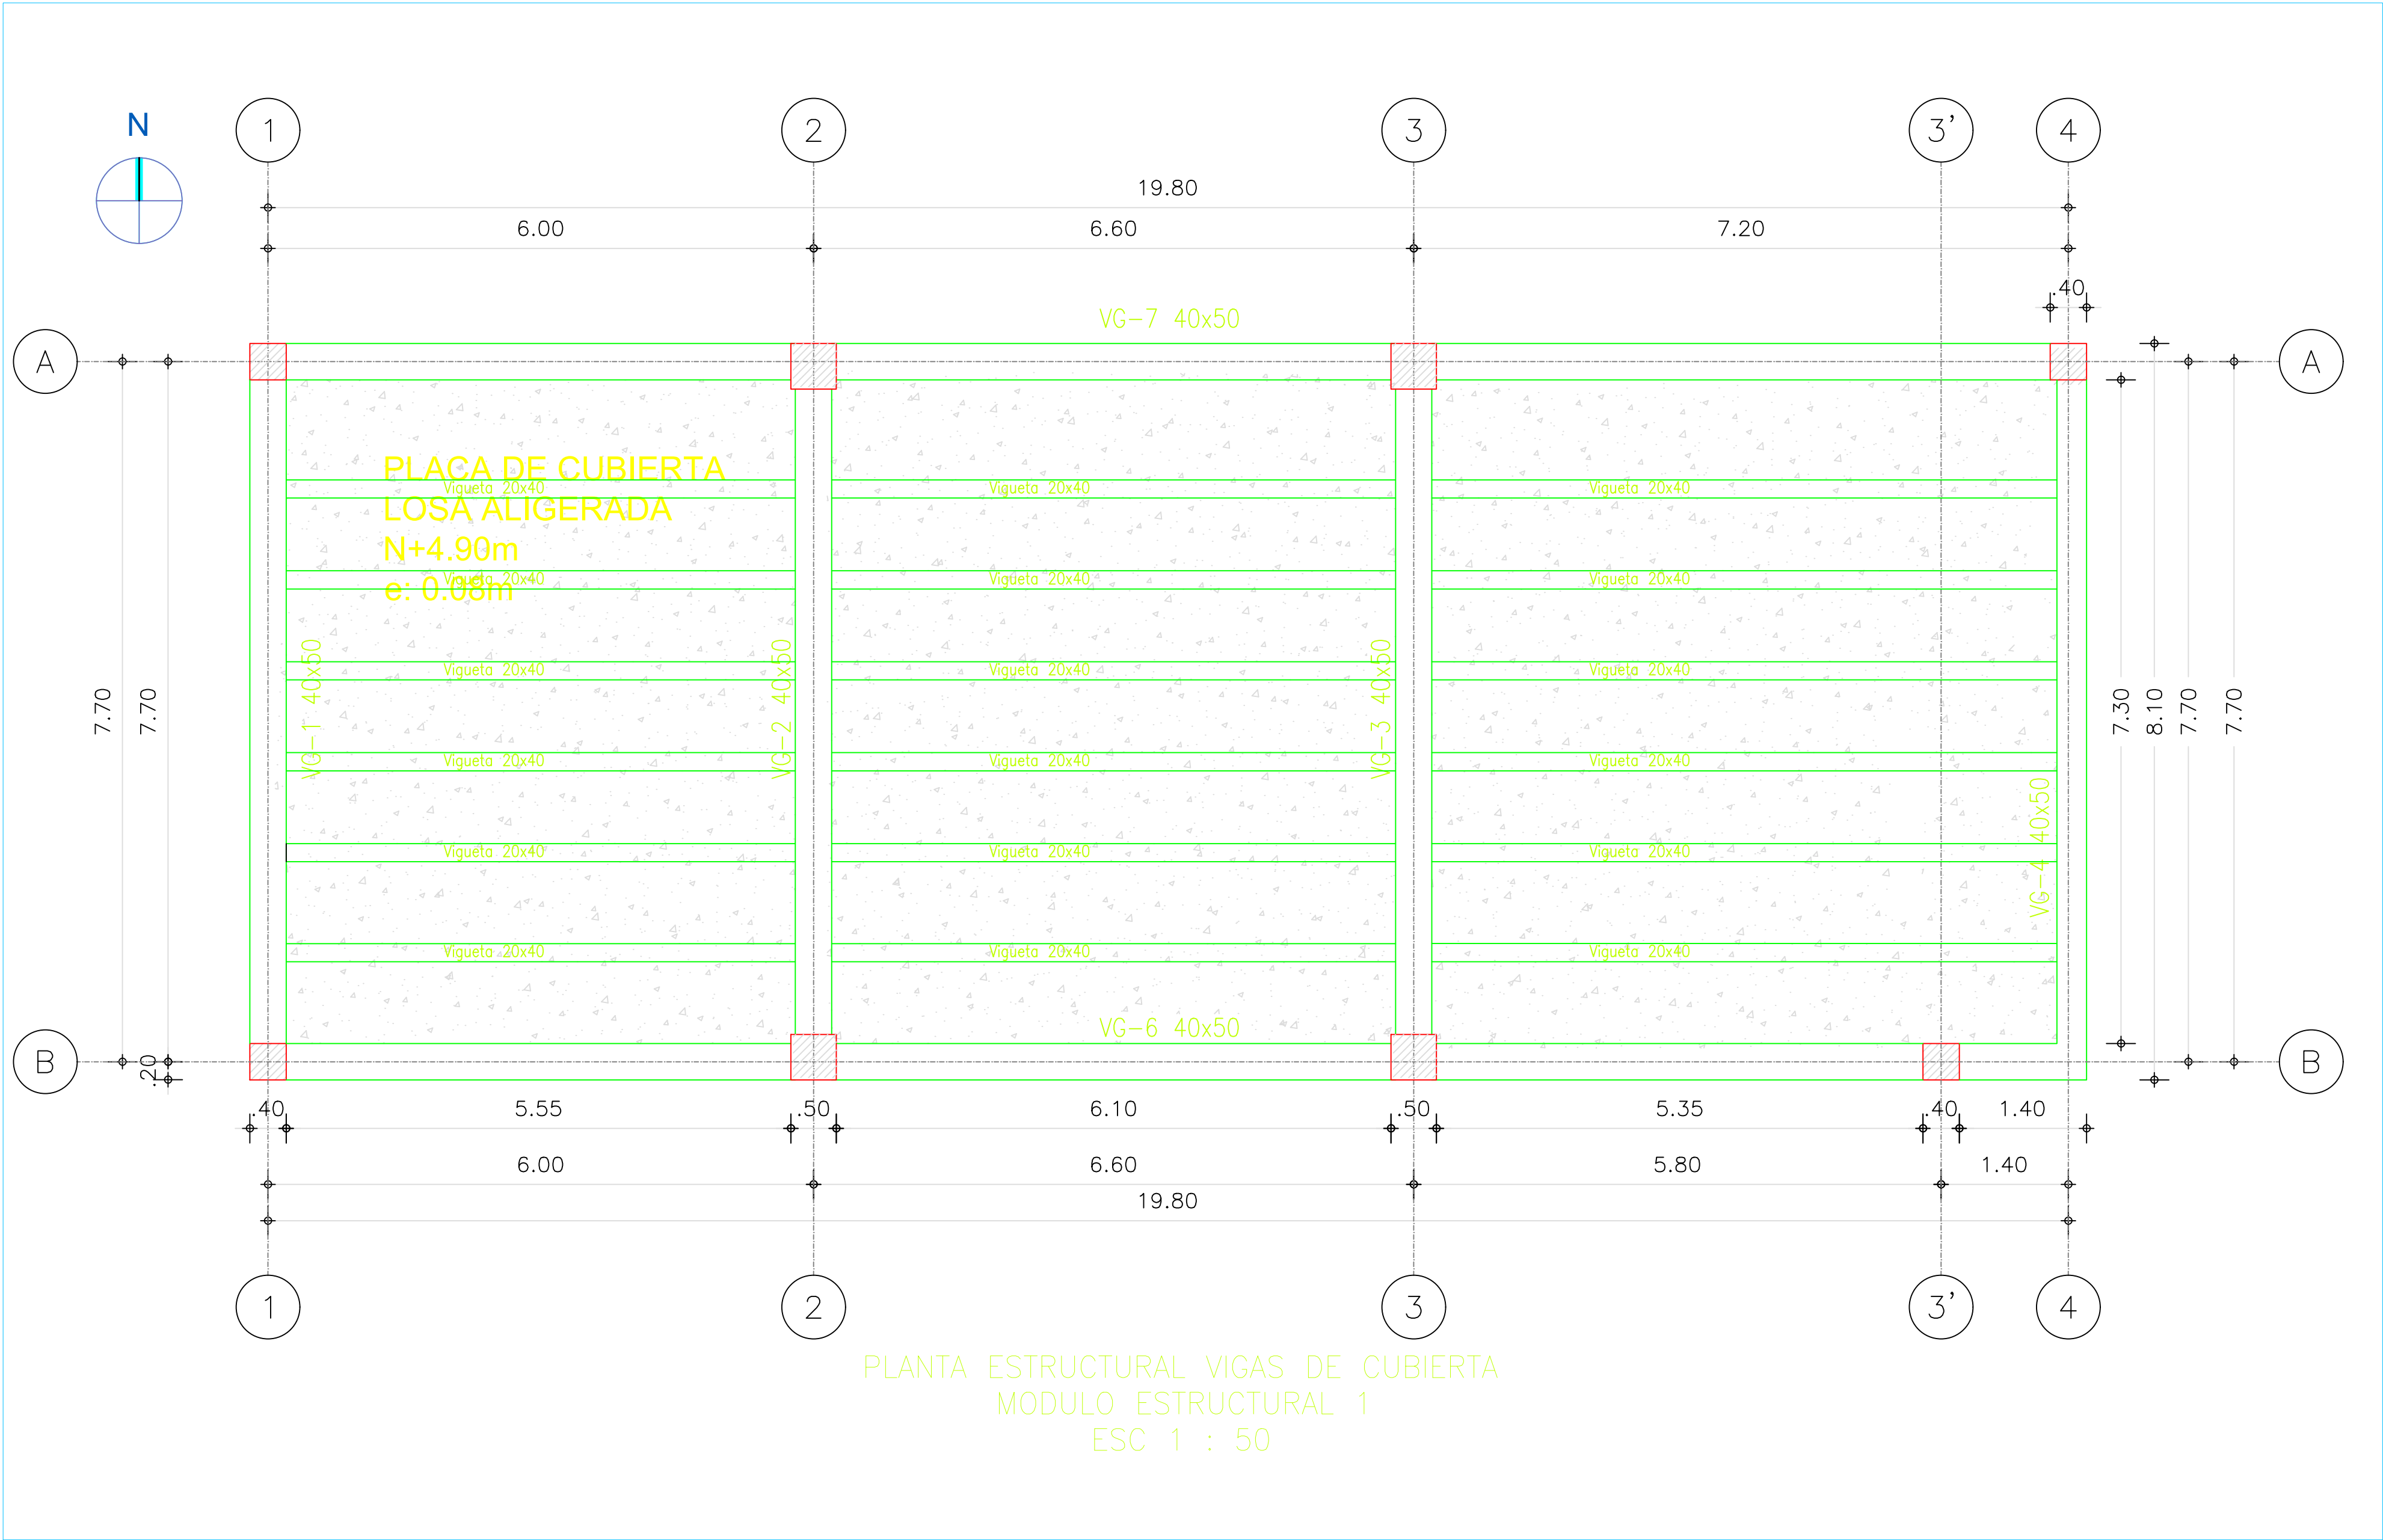
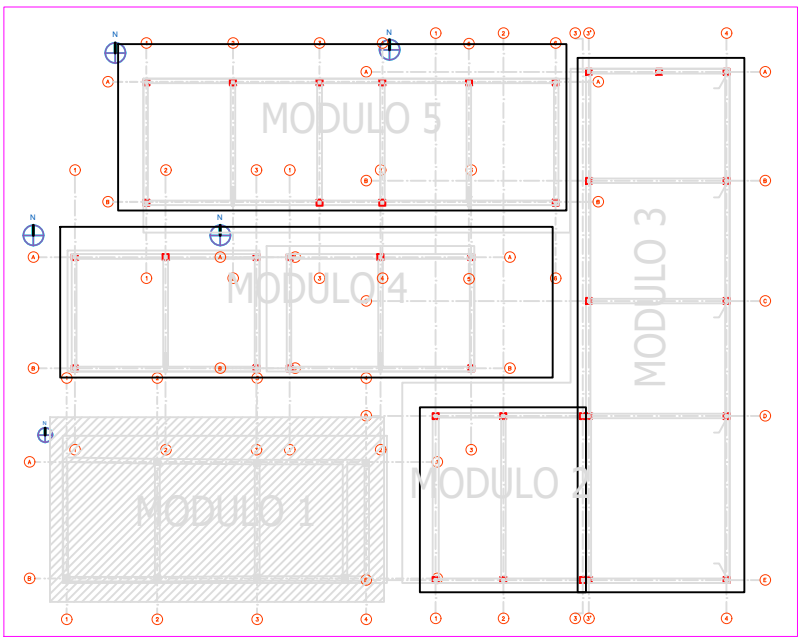
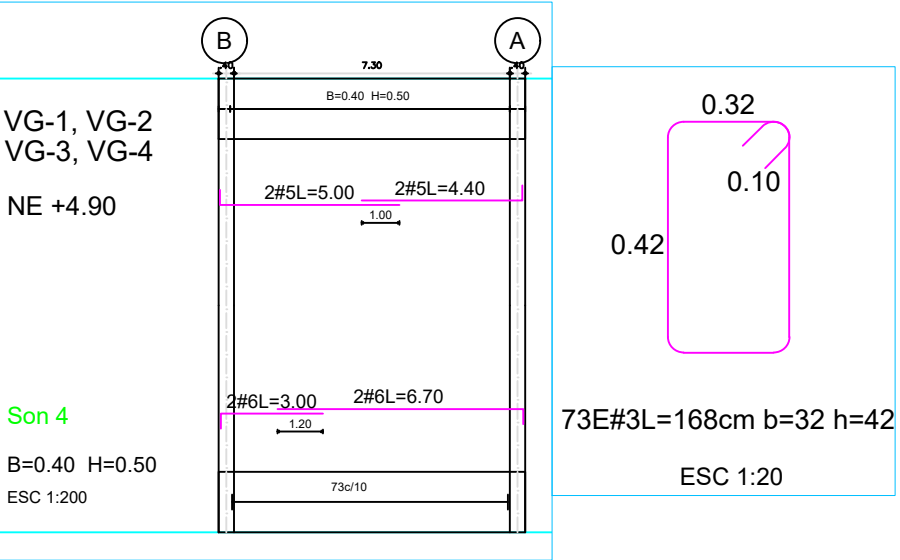


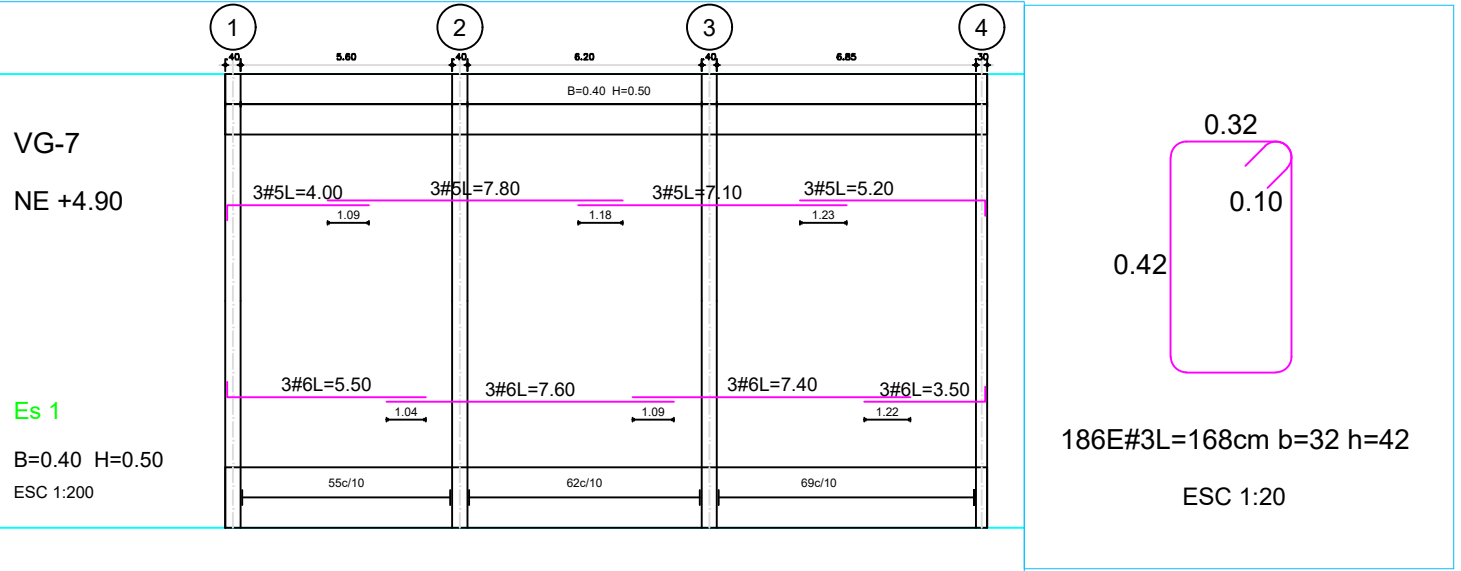

UBICACIÓN MODULO 1 Esc 1:500

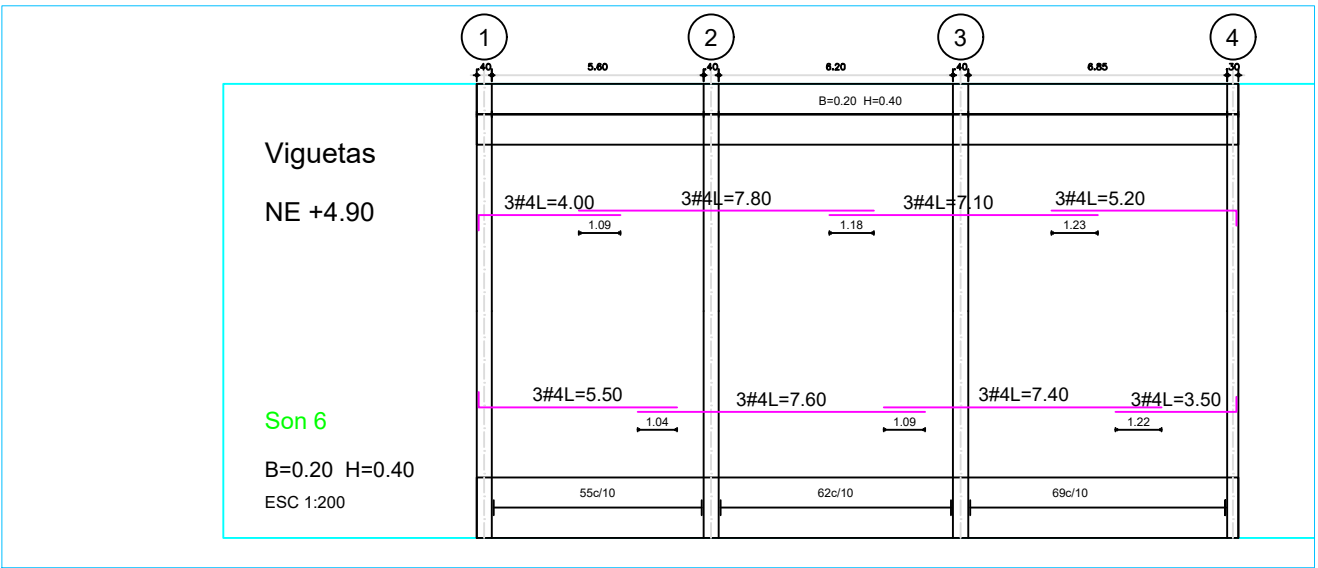

DESPIECE VIGAS DE CUBIERTA –MODULO ESTRUCTURAL 1–

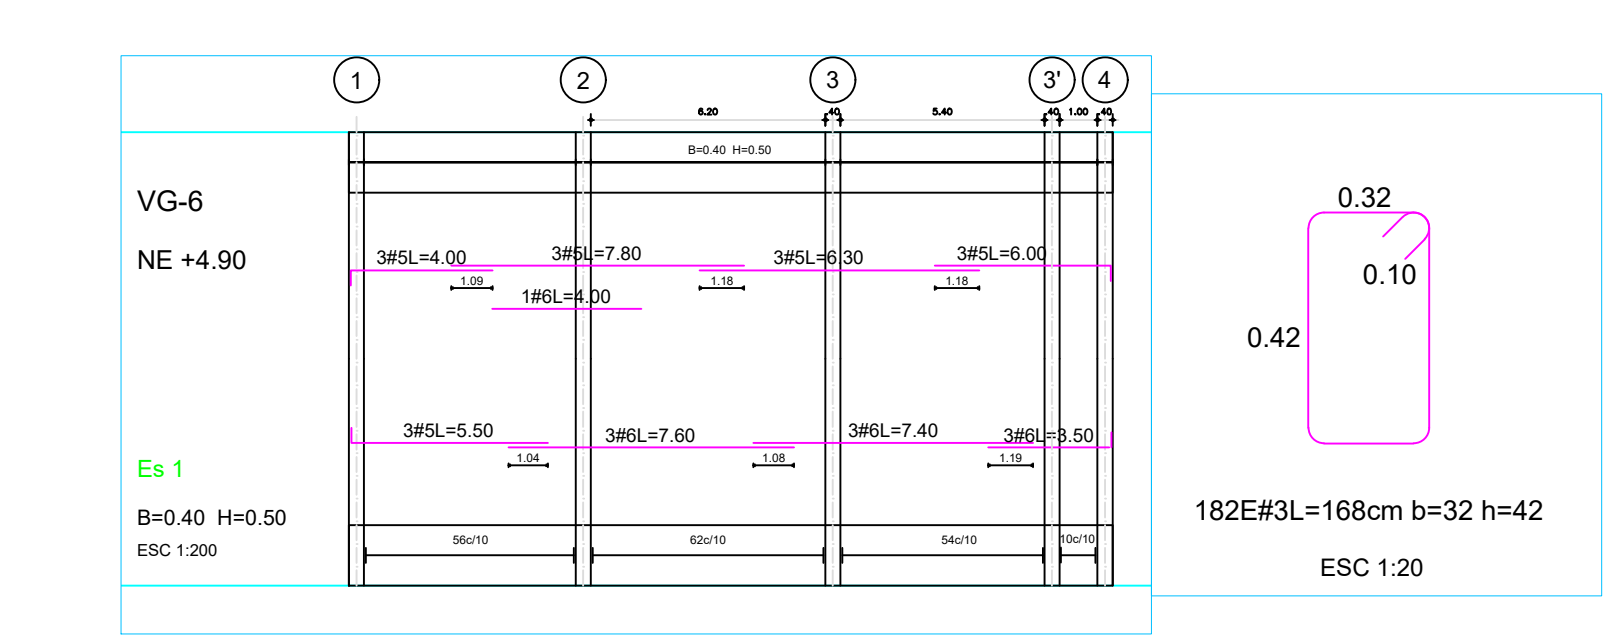

ESPECIFICACIONES TÉCNICAS			
LOCALIZACION:		COEFICIENTE DE IMPORTANCIA:	
NORMA DE DISEÑO: NSR-10		PERFIL DEL SUELO:	
AMENAZA SISMICA: ALTA		TIPO DE CIMENTACION: Superficial (Zapata aislada)	
SISTEMA DE RESISTENCIA SISMICA:		CAPACIDAD PORTANTE: 1.20 Kg/cm²	
PÓRTICOS DE CONCRETO REFORZADO		PROFUNDIDAD DE CIMENTACION:	
DISIPACION DE ENERGIA: ESPECIAL (DES)		MATERIALES:	CONCRETO Fc = 280 Kg/cm² (4.000 PSI)
VALORES:			ACERO DE REFUERZO Mallas electrosoldadas fy = 4200 Kg/cm² Refuerzo varillas Ø≥ 3/8" fy = 4200 Kg/cm² Refuerzo varillas Ø< 3/8" fy = 4200 Kg/cm²
GRUPO DE USO:			
Grupo III — Edificaciones de atención a la comunidad			
CARGAS			
CARGAS MUERTAS:		CARGAS VIVAS:	
Pendentado e impermeabilización placa maciza: 0.15 tn/m²		Pendiente de la cubierta liviana inferior a 15°: 0.05 tn/m²	
Cubierta liviana incluye teja y correas: 0.02 tn/m²		Carga de granizo con altitud inferior a 2000 msnm: 0.00 tn/m²	
CONVENCIONES			
C1 = COLUMNA DE CONFINAMIENTO NE = Nivel Estructural VC = Viga de Cimentación VG = Viga <u>Lectura de Refuerzo en elementos Estructurales:</u> 2#4L=4.60: Cantidad, número y longitud de la varilla 18E#3 L=90cm b=15 h=20: Cantidad, Estribo, número y longitud de la varilla, base y altura del estribo			
UNIDADES DE MEDIDA			
TODAS LAS UNIDADES DE MEDIDA, ESTÁN EXPRESADAS EN METROS, EXCEPTO LO INDICADO EN OTRAS UNIDADES			
CUADRO DE TRASLAPOS Y GANCHOS			
LONGITUD MINIMA DE TRASLAPO		LONGITUD MINIMA DE GANCHOS	
			
DIAMETRO Ø	LONGITUD (mt)	DIAMETRO Ø	LONGITUD (mt)
2	0.40	< 3	0.15
3	0.50	4	0.20
4	0.70	5	0.25
5	0.90	6	0.30
6	1.10	7	0.35
7	1.20	8	0.40