
N.G.

PLANTA DE COLUMNAS

ESCALA 1:75

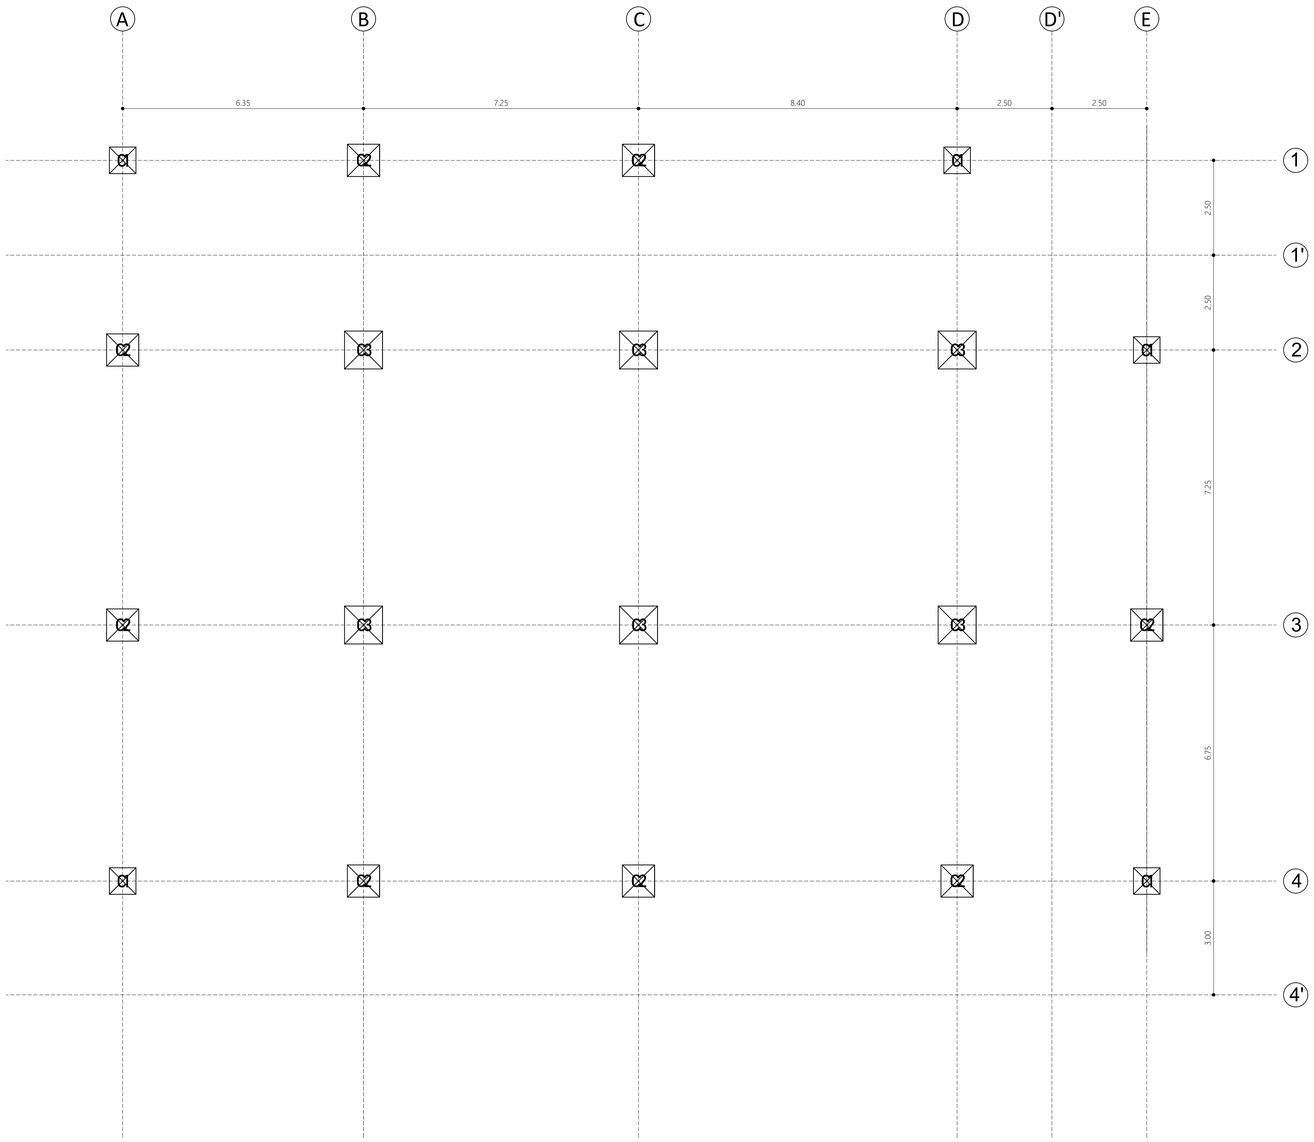

PARÁMETROS DE DISEÑO

1. Ciudad: Bogotá
2. Departamento: Cundinamarca
3. Grupo de Uso: (I) (Vivienda)
4. Coeficiente de Importancia: 1.00
5. Capacidad de Disipación de Energia: DMO
6. Zona de Amenaza Sísmica: Intermedia
7. Perfil de Suelo: Cerros
8. Parámetros Sísmicos: Aa=0.15 Av=0.20
   Fa=1.35 Fv=1.30

MATERIALES DE CONSTRUCCIÓN

CONCRETO ESTRUCTURAL

- Concreto de zapatas f'c=21.0 MPa
- Concreto de vigas de cimentación f'c=21.0 MPa
- Concreto de columnas f'c=21.0 MPa
- Concreto de vigas aéreas f'c=21.0 MPa
- Concreto de losas f'c=21.0 MPa


DIÁMETRO MÍNIMO DE DOBLADO

DIÁMETRO DE LAS BARRAS	DÍAMETRO DE DOBLADO
No.3(3/8") ó 10M(10mm) a No.8(1") ó 25M(25mm)	6db
No.9(1-1/8") ó 30M(30mm), No.10(1-1/4") ó 32M(32mm) y No.11(1-3/8") ó 36M(36mm)	8db
No.14(1-3/4") ó 45M(45mm) y No.18(2-1/4") ó 55M(55mm)	10db

ACERO ESTRUCTURAL

- Acero de refuerzo Fy=420 MPa

COLUMNAS

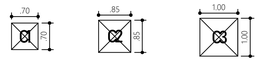

UNIVERSIDAD NACIONAL DE COLOMBIA

Proyecto:

EDIFICIO OFICINAS UNIVERSIDAD NACIONAL GRUPO 2

Diseñó:

Nota: Por medio de la presente, manifiesto que los planos estructurales han sido elaborados de conformidad con los requisitos establecidos en el Reglamento Colombiano de Construcción Sismo Resistente NSR-10 y demás disposiciones técnicas aplicables.

Asimismo, dejo constancia de que el diseño estructural contenido en estos planos es de mi exclusiva responsabilidad profesional, por lo cual eximo a la entidad o al profesional encargado de la revisión del proyecto de cualquier responsabilidad derivada del diseño estructural aquí desarrollado.

XXXXXXXXXXXXXXXXXXXXXXXXXXX
ING. CIVIL M.P. XXXXXX CND.

Vo.Bo. Ing. Geotecnista

XXXXXXXXXX
XXXXXXXXXX

Dibujó:

DFBT

Contiene:

Planta general de columnas

Piso 1:
C1 70x70
C2 85x85
C3 100x100

Entrepisos:
C1 70x70
C2 85X85
C3 100X100

Archivo:
PRIMERA ENTREGA GRUPO 2.dwg

Fecha:
OCTUBRE 2026

VERSIÓN:

#	Mes	Año	Comentario
01	10	26	

Escala:

INDICADA

Plano
E


De:
5

N°:
1

ALZADO DE COLUMNAS


Corte A-A

ESCALA 1:75

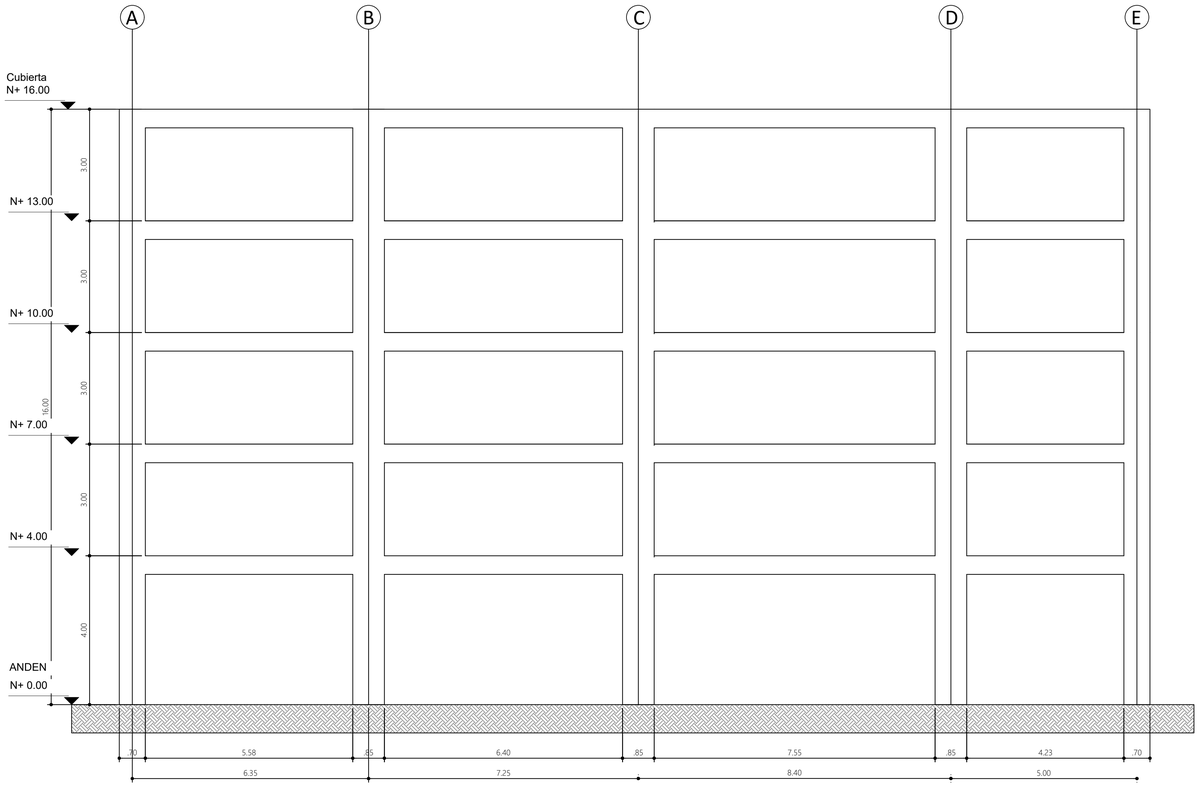


Corte B-B

ESCALA 1:75

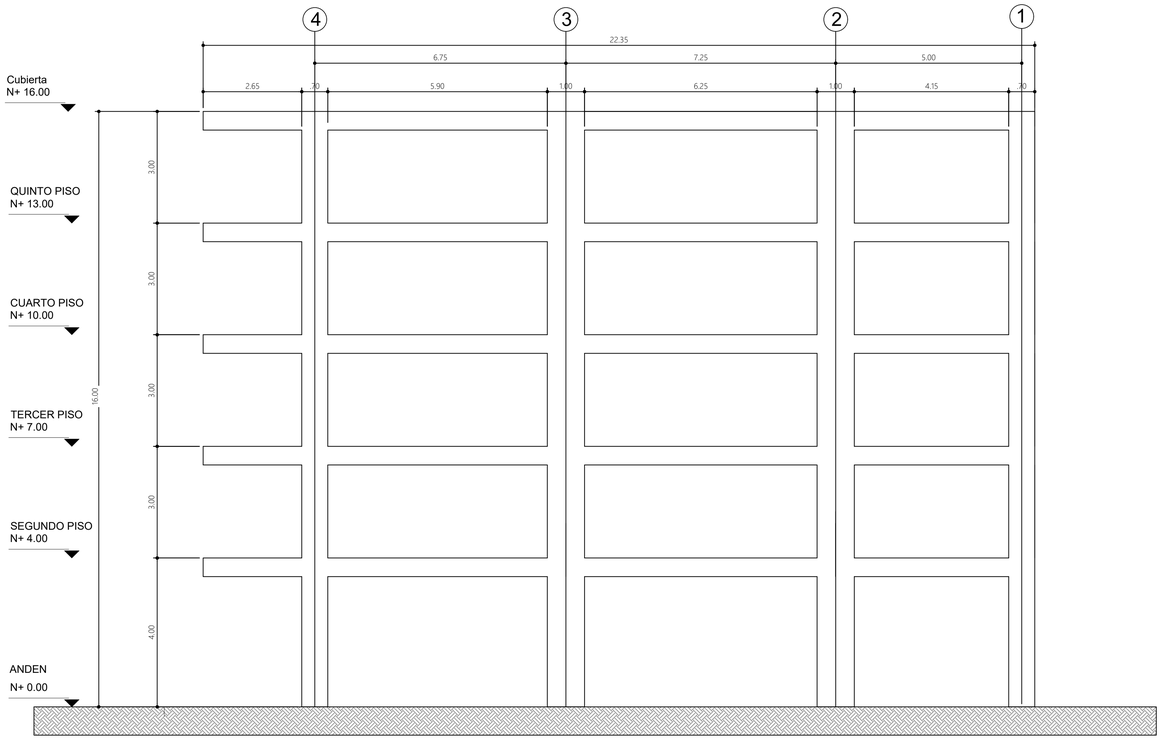

DETALLE ELEMENTOS NO ESTRUCTURALES


ESC 1:50

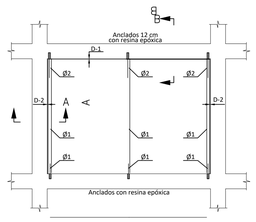

S	La separación máxima entre columnetas es de 2.00 m.
D-1	Dilatación 1 cm (dejar icopor ó similar de 1 cm).
D-2	Dilatación 1.5 cm (dejar icopor ó similar de 1.5 cm).
Ø1	1/2"
Ø2	1/2"

ELEMENTOS DE FACHADA CON TOLETE A LA VISTA CON ENCHAPE EN COLUMNAS Y VIGAS


ESC 1:50

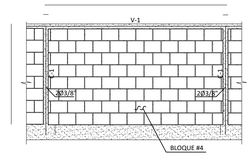

C-1	Columneta de 0.15x0.10
V-1	Cinta de 0.15x0.10


MUROS INTERNOS

ESC 1:50

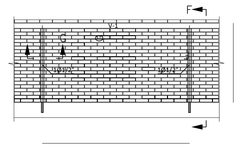

ANTEPECHOS Y PARAPETOS DE FACHADA EN LADRILLO DE PERFORACION VERTICAL

ESC 1:50

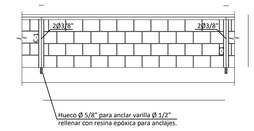

ANTEPECHOS EN BLOQUE No.4 CON PAÑETE

ESC 1:50

S	La separación máxima entre anclajes es de 1.50 m.
D-1	Dilatación 1 cm (dejar icopor ó similar de 1 cm).
D-2	Dilatación 1.5 cm (dejar icopor ó similar de 1.5 cm).
R-2	1Ø1/2" L=30cm anclada 8cm con resina epóxica.

ELEMENTOS INTERIORES ENMARCADOS EN PLACA Y COLUMNAS (BLOQUE #5) GRADO DE DESEMPEÑO BUENO

ESC 1:50


S	La separación máxima entre dovelas es de1.50 m.
D-1	Dilatación 1 cm (dejar icopor ó similar de 1 cm).
D-2	Dilatación 1.5 cm (dejar icopor ó similar de 1.5 cm).
	Dovela rellena con grouting

ELEMENTOS DE FACHADA CON LADRILLO DE PERFORACION VERTICAL

ESC 1:50

DETALLE ELEMENTOS NO ESTRUCTURALES


ESC 1:50

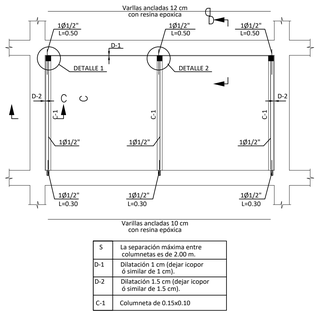

S	La separación máxima entre columnetas es de 2.00 m.
D-1	Dilatación 1 cm (dejar icopor ó similar de 1 cm).
D-2	Dilatación 1.5 cm (dejar icopor ó similar de 1.5 cm).
C-1	Columneta de 0.15x0.10

ELEMENTOS DE FACHADA CON PAÑETE EN BLOQUE #4

ESC 1:50

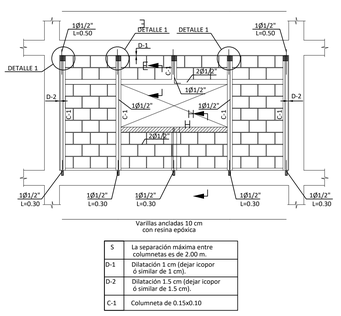

S	La separación máxima entre columnetas es de 2.00 m.
D-1	Dilatación 1 cm (dejar icopor ó similar de 1 cm).
D-2	Dilatación 1.5 cm (dejar icopor ó similar de 1.5 cm).
C-1	Columneta de 0.15x0.10

ELEMENTOS DE FACHADA CON PAÑETE EN BLOQUE #4 CON VENTANA

ESC 1:50

UNIVERSIDAD NACIONAL DE COLOMBIA

Proyecto:

EDIFICIO OFICINAS UNIVERSIDAD NACIONAL GRUPO 2

Diseñó:

Nota: Por medio de la presente, manifiesto que los planos estructurales han sido elaborados de conformidad con los requisitos establecidos en el Reglamento Colombiano de Construcción Sismo Resistente NSR-10 y demás disposiciones técnicas aplicables.

Asimismo, dejo constancia de que el diseño estructural contenido en estos planos es de mi exclusiva responsabilidad profesional, por lo cual eximo a la entidad o al profesional encargado de la revisión del proyecto de cualquier responsabilidad derivada del diseño estructural aquí desarrollado.

XXXXXXXXXXXXXXXXXXXXXXXXXXX
ING. CIVIL M.P. XXXXXX CND.

Vo.Bo. Ing. Geotecnista

XXXXXXXXXX
XXXXXXXXXX

Dibujó:

DFBH

Contiene:

Corte A-A y B-B

Alzado de columnas

Detalles generales de elementos no estructurales.

Archivo:

PRIMERA ENTREGA GRUPO 2.dwg

Fecha:

OCTUBRE 2026

VERSIÓN:

#	Mes	Año	Comentario
01	10	26	

Escala:

INDICADA

Plano

E

De:

5


N°:


2

N.G.

PLANTA ESTRUCTURAL DE CIMENTACIÓN

ESCALA 1:75

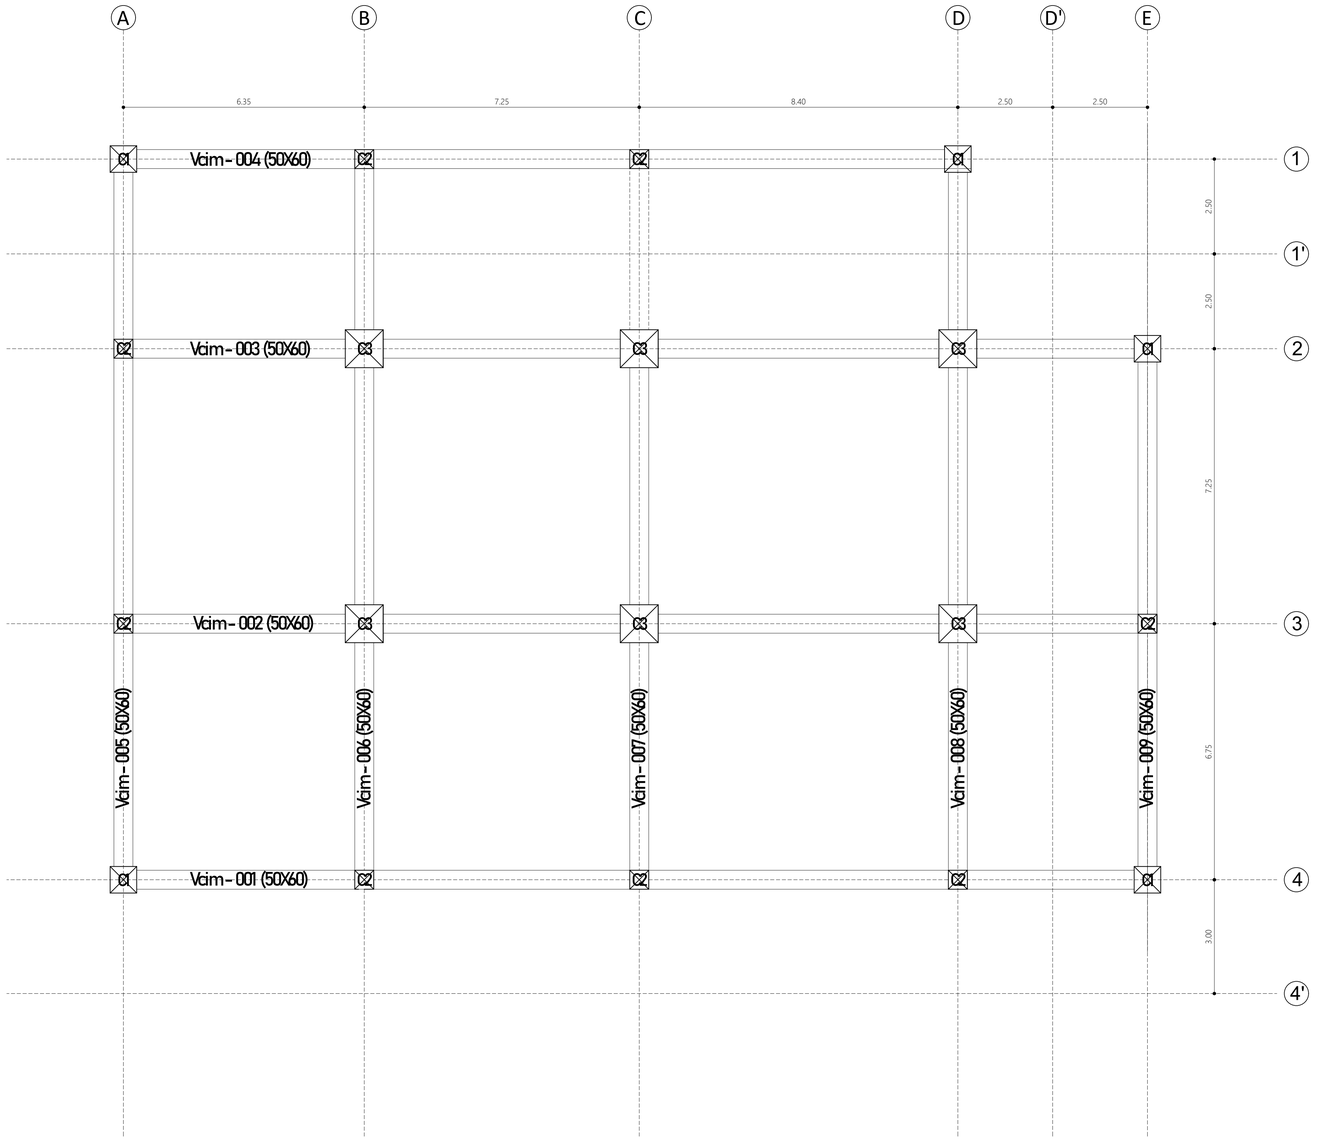

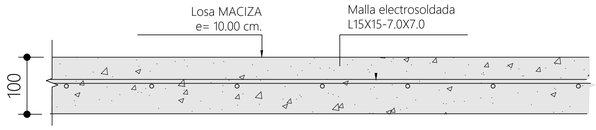

DETALLE DE LOSA MACIZA DE CONTRAPISO
ESCALA 1:1

PARÁMETROS DE DISEÑO

1. Ciudad: Bogotá
2. Departamento: Cundinamarca
3. Grupo de Uso: (I) (Vivienda)
4. Coeficiente de Importancia: 1.00
5. Capacidad de Disipación de Energia: DMO
6. Zona de Amenaza Sísmica: Intermedia
7. Perfil de Suelo: Cerros
8. Parámetros Sísmicos: Aa=0.15 Av=0.20
   Fa=1.35 Fv=1.30

MATERIALES DE CONSTRUCCIÓN

CONCRETO ESTRUCTURAL

- Concreto de zapatas f'c=21.0 MPa
- Concreto de vigas de cimentación f'c=21.0 MPa
- Concreto de columnas f'c=21.0 MPa
- Concreto de vigas aéreas f'c=21.0 MPa
- Concreto de losas f'c=21.0 MPa


DIÁMETRO MÍNIMO DE DOBLADO

DIÁMETRO DE LAS BARRAS	DÍAMETRO DE DOBLADO
No.3(3/8") ó 10M(10mm) a No.8(1") ó 25M(25mm)	6db
No.9(1-1/8") ó 30M(30mm), No.10(1-1/4") ó 32M(32mm) y No.11(1-3/8") ó 36M(36mm)	8db
No.14(1-3/4") ó 45M(45mm) y No.18(2-1/4") ó 55M(55mm)	10db

ACERO ESTRUCTURAL

- Acero de refuerzo Fy=420 MPa

COLUMNAS

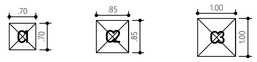

UNIVERSIDAD NACIONAL DE COLOMBIA

Proyecto:

EDIFICIO OFICINAS UNIVERSIDAD NACIONAL GRUPO 2

Diseñó:

Nota: Por medio de la presente, manifiesto que los planos estructurales han sido elaborados de conformidad con los requisitos establecidos en el Reglamento Colombiano de Construcción Sismo Resistente NSR-10 y demás disposiciones técnicas aplicables.

Asimismo, dejo constancia de que el diseño estructural contenido en estos planos es de mi exclusiva responsabilidad profesional, por lo cual eximo a la entidad o al profesional encargado de la revisión del proyecto de cualquier responsabilidad derivada del diseño estructural aquí desarrollado.

XXXXXXXXXXXXXXXXXXXXXXXXXXX
ING. CIVIL M.P. XXXXXX CND.

Vo.Bo. Ing. Geotecnista

XXXXXXXXXX
XXXXXXXXXX

Dibujó:

DFBF

Contiene:

Planta general de vigas de cimentación

Detalle y despiece de la losa de contrapiso

Detalles generales de zapatas

profundidad de desplante 1.50 m

Capacidad Portante 210 kPa

Archivo:
PRIMERA ENTREGA GRUPO 2.dwg

Fecha:
JULIO 2026

VERSIÓN:

#	Mes	Año	Comentario
01	10	26	

Escala:

INDICADA


Plano
E

De:
5


N°:
3

N.G.

PLANTA ESTRUCTURAL DE PRIMER PISO
ESCALA 1:75

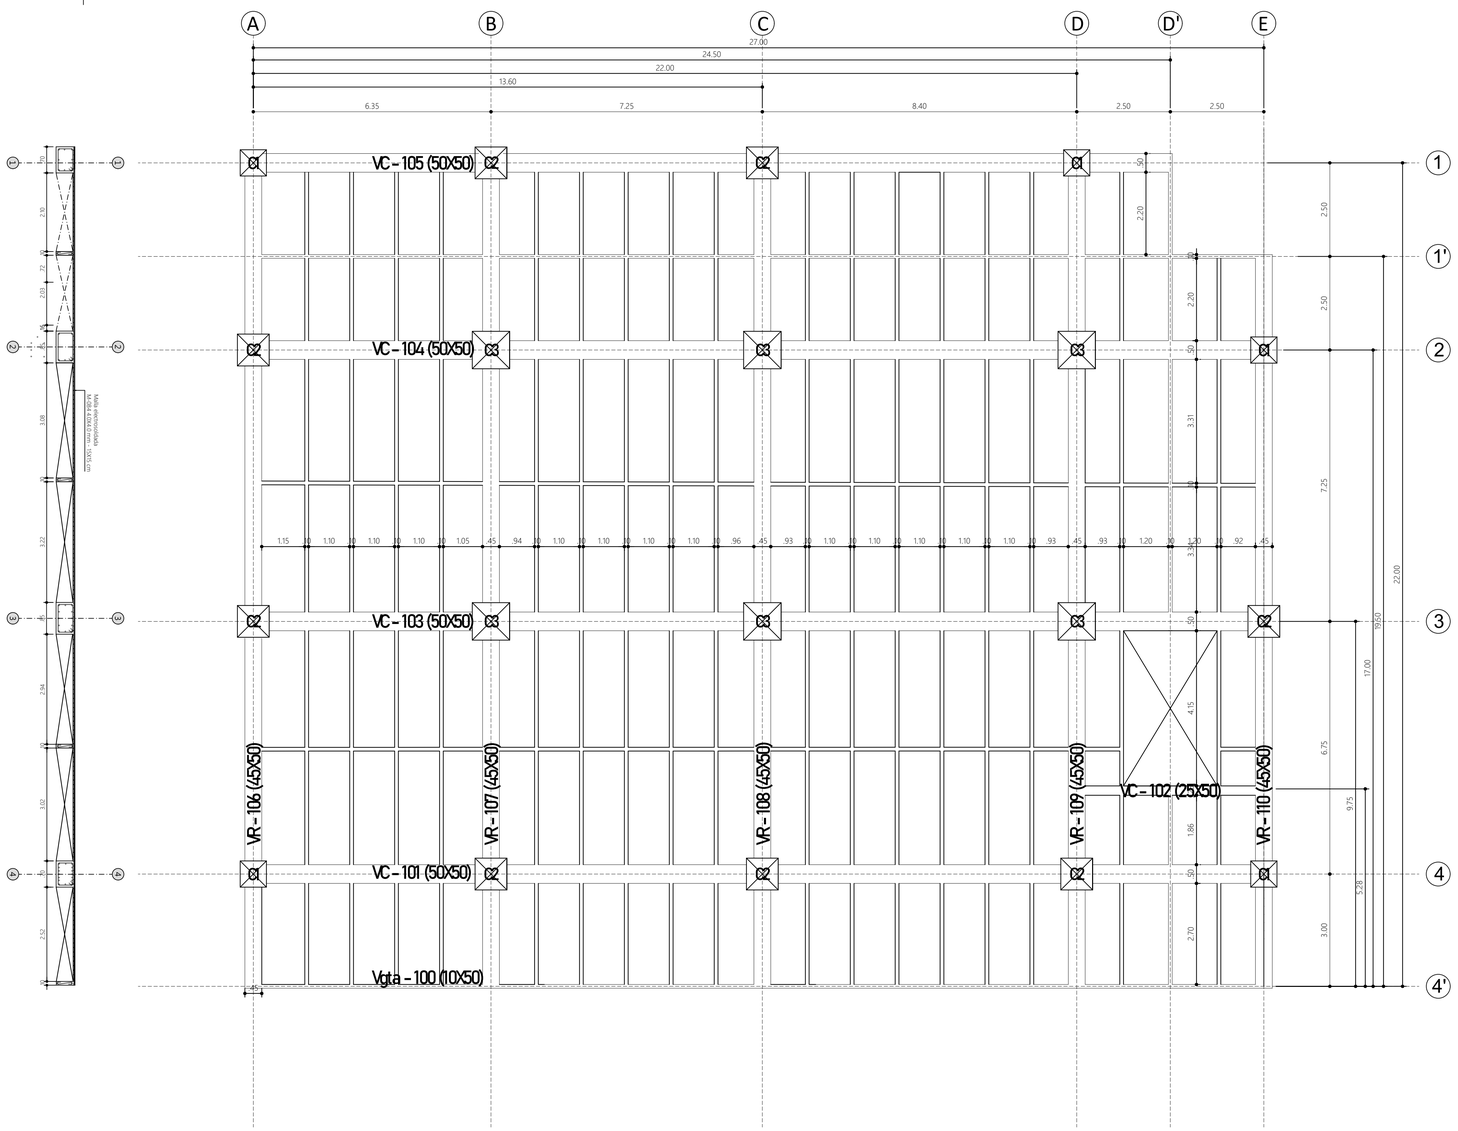

CORTE ESTRUCTURAL TIPO
ESCALA 1:75

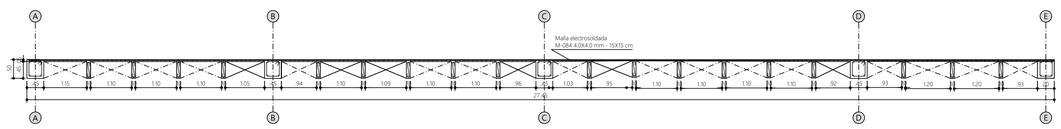

CORTE ESTRUCTURAL TIPO
ESCALA 1:75

PARÁMETROS DE DISEÑO

1. Ciudad: Bogotá
2. Departamento: Cundinamarca
3. Grupo de Uso: (I) (Vivienda)
4. Coeficiente de Importancia: 1.00
5. Capacidad de Disipación de Energia: DMO
6. Zona de Amenaza Sísmica: Intermedia
7. Perfil de Suelo: Cerros
8. Parámetros Sísmicos: Aa=0.15 Av=0.20
   Fa=1.35 Fv=1.30

MATERIALES DE CONSTRUCCIÓN

CONCRETO ESTRUCTURAL

- Concreto de zapatas f'c=21.0 MPa
- Concreto de vigas de cimentación f'c=21.0 MPa
- Concreto de columnas f'c=21.0 MPa
- Concreto de vigas aéreas f'c=21.0 MPa
- Concreto de losas f'c=21.0 MPa


DIÁMETRO MÍNIMO DE DOBLADO

DIÁMETRO DE LAS BARRAS	DÍAMETRO DE DOBLADO
No.3(3/8") ó 10M(10mm) a No.8(1") ó 25M(25mm)	6db
No.9(1-1/8") ó 30M(30mm), No.10(1-1/4") ó 32M(32mm) y No.11(1-3/8") ó 36M(36mm)	8db
No.14(1-3/4") ó 45M(45mm) y No.18(2-1/4") ó 55M(55mm)	10db


ACERO ESTRUCTURAL

- Acero de refuerzo Fy=420 MPa


COLUMNAS

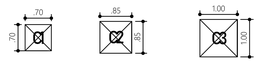

DETALLE RIOSTRA
ESCALA 1:50

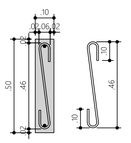

DETALLE VIGUETA
ESCALA 1:50

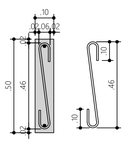

UNIVERSIDAD NACIONAL DE COLOMBIA

Proyecto:

EDIFICIO OFICINAS UNIVERSIDAD NACIONAL GRUPO 2

Diseñó:

Nota: Por medio de la presente, manifiesto que los planos estructurales han sido elaborados de conformidad con los requisitos establecidos en el Reglamento Colombiano de Construcción Sismo Resistente NSR-10 y demás disposiciones técnicas aplicables.

Asimismo, dejo constancia de que el diseño estructural contenido en estos planos es de mi exclusiva responsabilidad profesional, por lo cual eximo a la entidad o al profesional encargado de la revisión del proyecto de cualquier responsabilidad derivada del diseño estructural aquí desarrollado.

XXXXXXXXXXXXXXXXXXXXXXXXXXX
ING. CIVIL M.P. XXXXXX CND.

Vo.Bo. Ing. Geotecnista

XXXXXXXXXX
XXXXXXXXXX

Dibujó:

DFBF

Contiene:

Planta general del primer piso

Detalle y despiece de la losa

Detalles despiece de escalera.

Archivo:
PRIMERA ENTREGA GRUPO 2.dwg

Fecha:
OCTUBRE 2026

VERSIÓN:			
#	Mes	Año	Comentario
01	10	26	

Escala:

INDICADA

Plano
E


De:
5


N°:
4

N.G.

PLANTA ESTRUCTURAL DE PISO TIPO

ESCALA 1:75

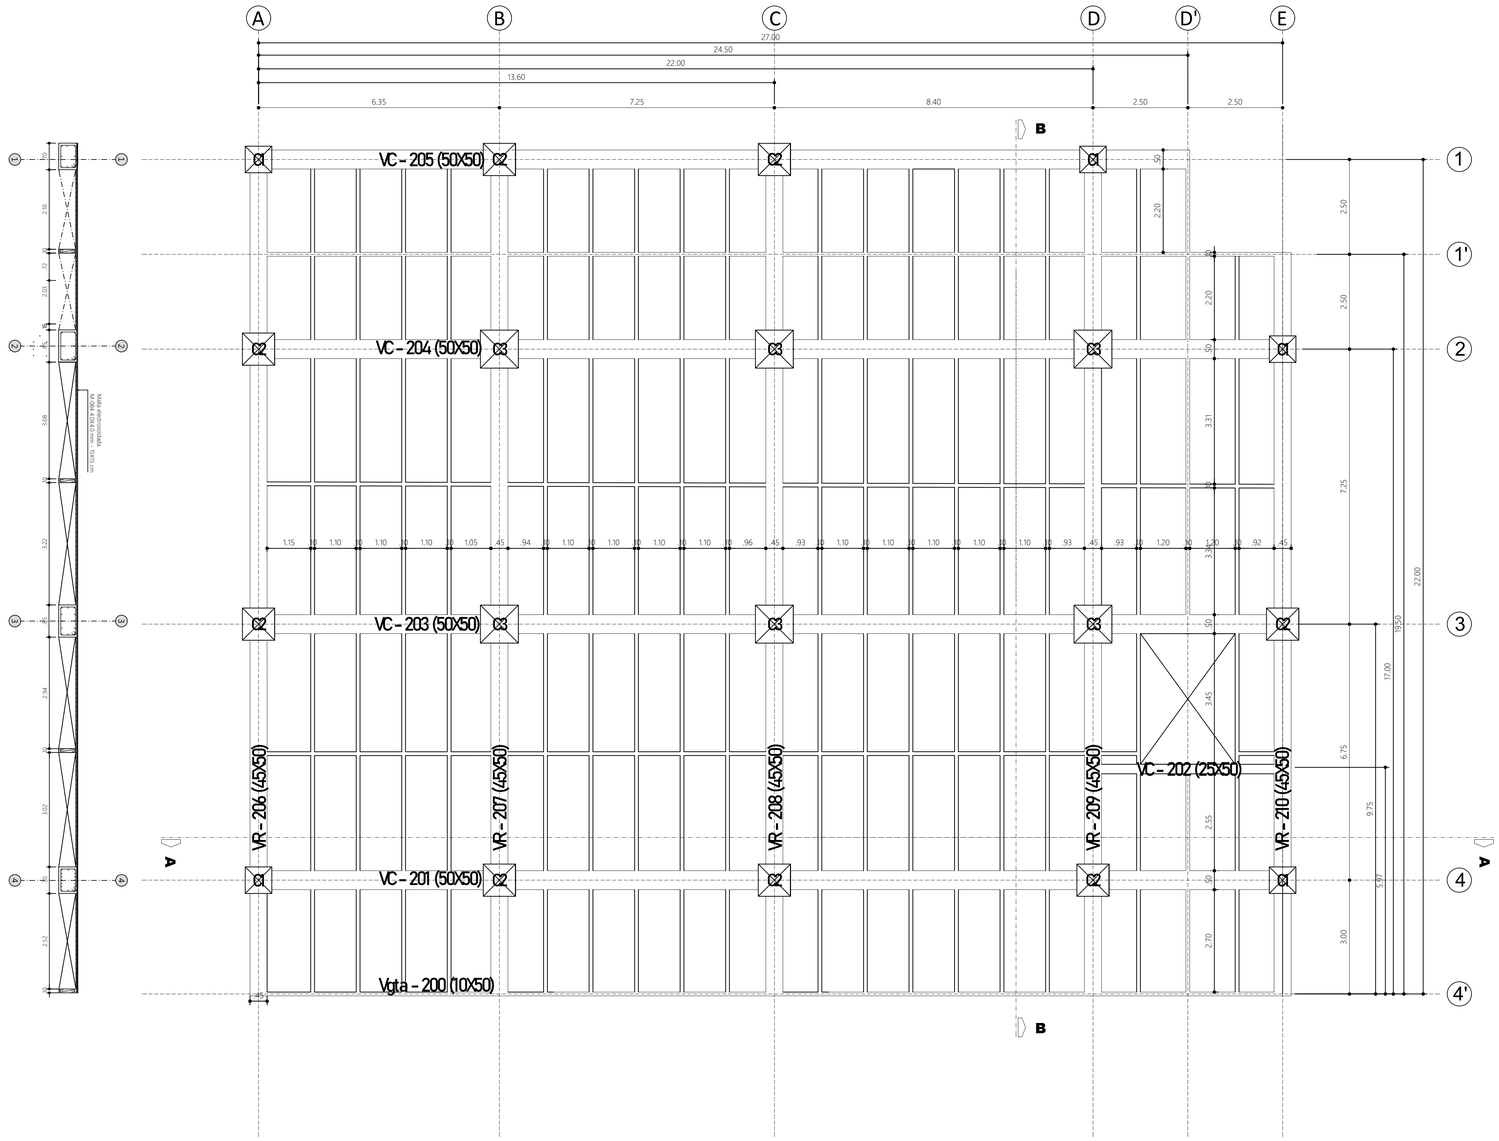

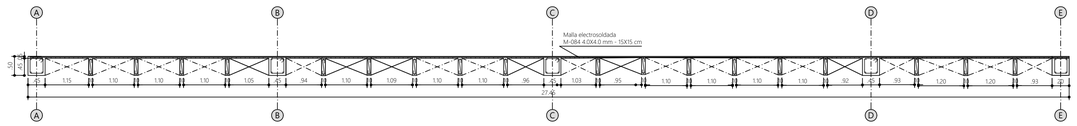

CORTE ESTRUCTURAL TIPO
ESCALA 1:75

PARÁMETROS DE DISEÑO

1. Ciudad: Bogotá
2. Departamento: Cundinamarca
3. Grupo de Uso: (I) (Vivienda)
4. Coeficiente de Importancia: 1.00
5. Capacidad de Disipación de Energia: DMO
6. Zona de Amenaza Sísmica: Intermedia
7. Perfil de Suelo: Cerros
8. Parámetros Sísmicos: Aa=0.15 Av=0.20
   Fa=1.35 Fv=1.30

MATERIALES DE CONSTRUCCIÓN

CONCRETO ESTRUCTURAL

- Concreto de zapatas f'c=21.0 MPa
- Concreto de vigas de cimentación f'c=21.0 MPa
- Concreto de columnas f'c=21.0 MPa
- Concreto de vigas aéreas f'c=21.0 MPa
- Concreto de losas f'c=21.0 MPa


DIÁMETRO MÍNIMO DE DOBLADO

DIÁMETRO DE LAS BARRAS	DÍAMETRO DE DOBLADO
No.3(3/8") ó 10M(10mm) a No.8(1") ó 25M(25mm)	6db
No.9(1-1/8") ó 30M(30mm), No.10(1-1/4") ó 32M(32mm) y No.11(1-3/8") ó 36M(36mm)	8db
No.14(1-3/4") ó 45M(45mm) y No.18(2-1/4") ó 55M(55mm)	10db


ACERO ESTRUCTURAL

- Acero de refuerzo Fy=420 MPa


COLUMNAS

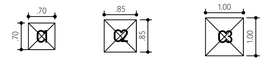

DETALLE RIOSTRA
ESCALA 1:50

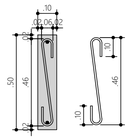

DETALLE VIGUETA
ESCALA 1:50

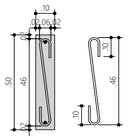

UNIVERSIDAD NACIONAL DE COLOMBIA

Proyecto:

EDIFICIO OFICINAS UNIVERSIDAD NACIONAL GRUPO 2

Diseñó:

Nota: Por medio de la presente, manifiesto que los planos estructurales han sido elaborados de conformidad con los requisitos establecidos en el Reglamento Colombiano de Construcción Sismo Resistente NSR-10 y demás disposiciones técnicas aplicables.

Asimismo, dejo constancia de que el diseño estructural contenido en estos planos es de mi exclusiva responsabilidad profesional, por lo cual eximo a la entidad o al profesional encargado de la revisión del proyecto de cualquier responsabilidad derivada del diseño estructural aquí desarrollado.

XXXXXXXXXXXXXXXXXXXXXXXXXXX
ING. CIVIL M.P. XXXXXX CND.

Vo.Bo. Ing. Geotecnista

XXXXXXXXXX
XXXXXXXXXX

Dibujó:

DFBF

Contiene:

Planta general del segundo piso

Detalle y despiece de la losa

Detalles generales y despiece de escalera

Archivo:

PRIMERA ENTREGA GRUPO 2.dwg

Fecha:

JULIO 2026

VERSIÓN:

#	Mes	Año	Comentario
01	10	26	

Escala:

INDICADA

Plano

E

De:

5

N°:

5