




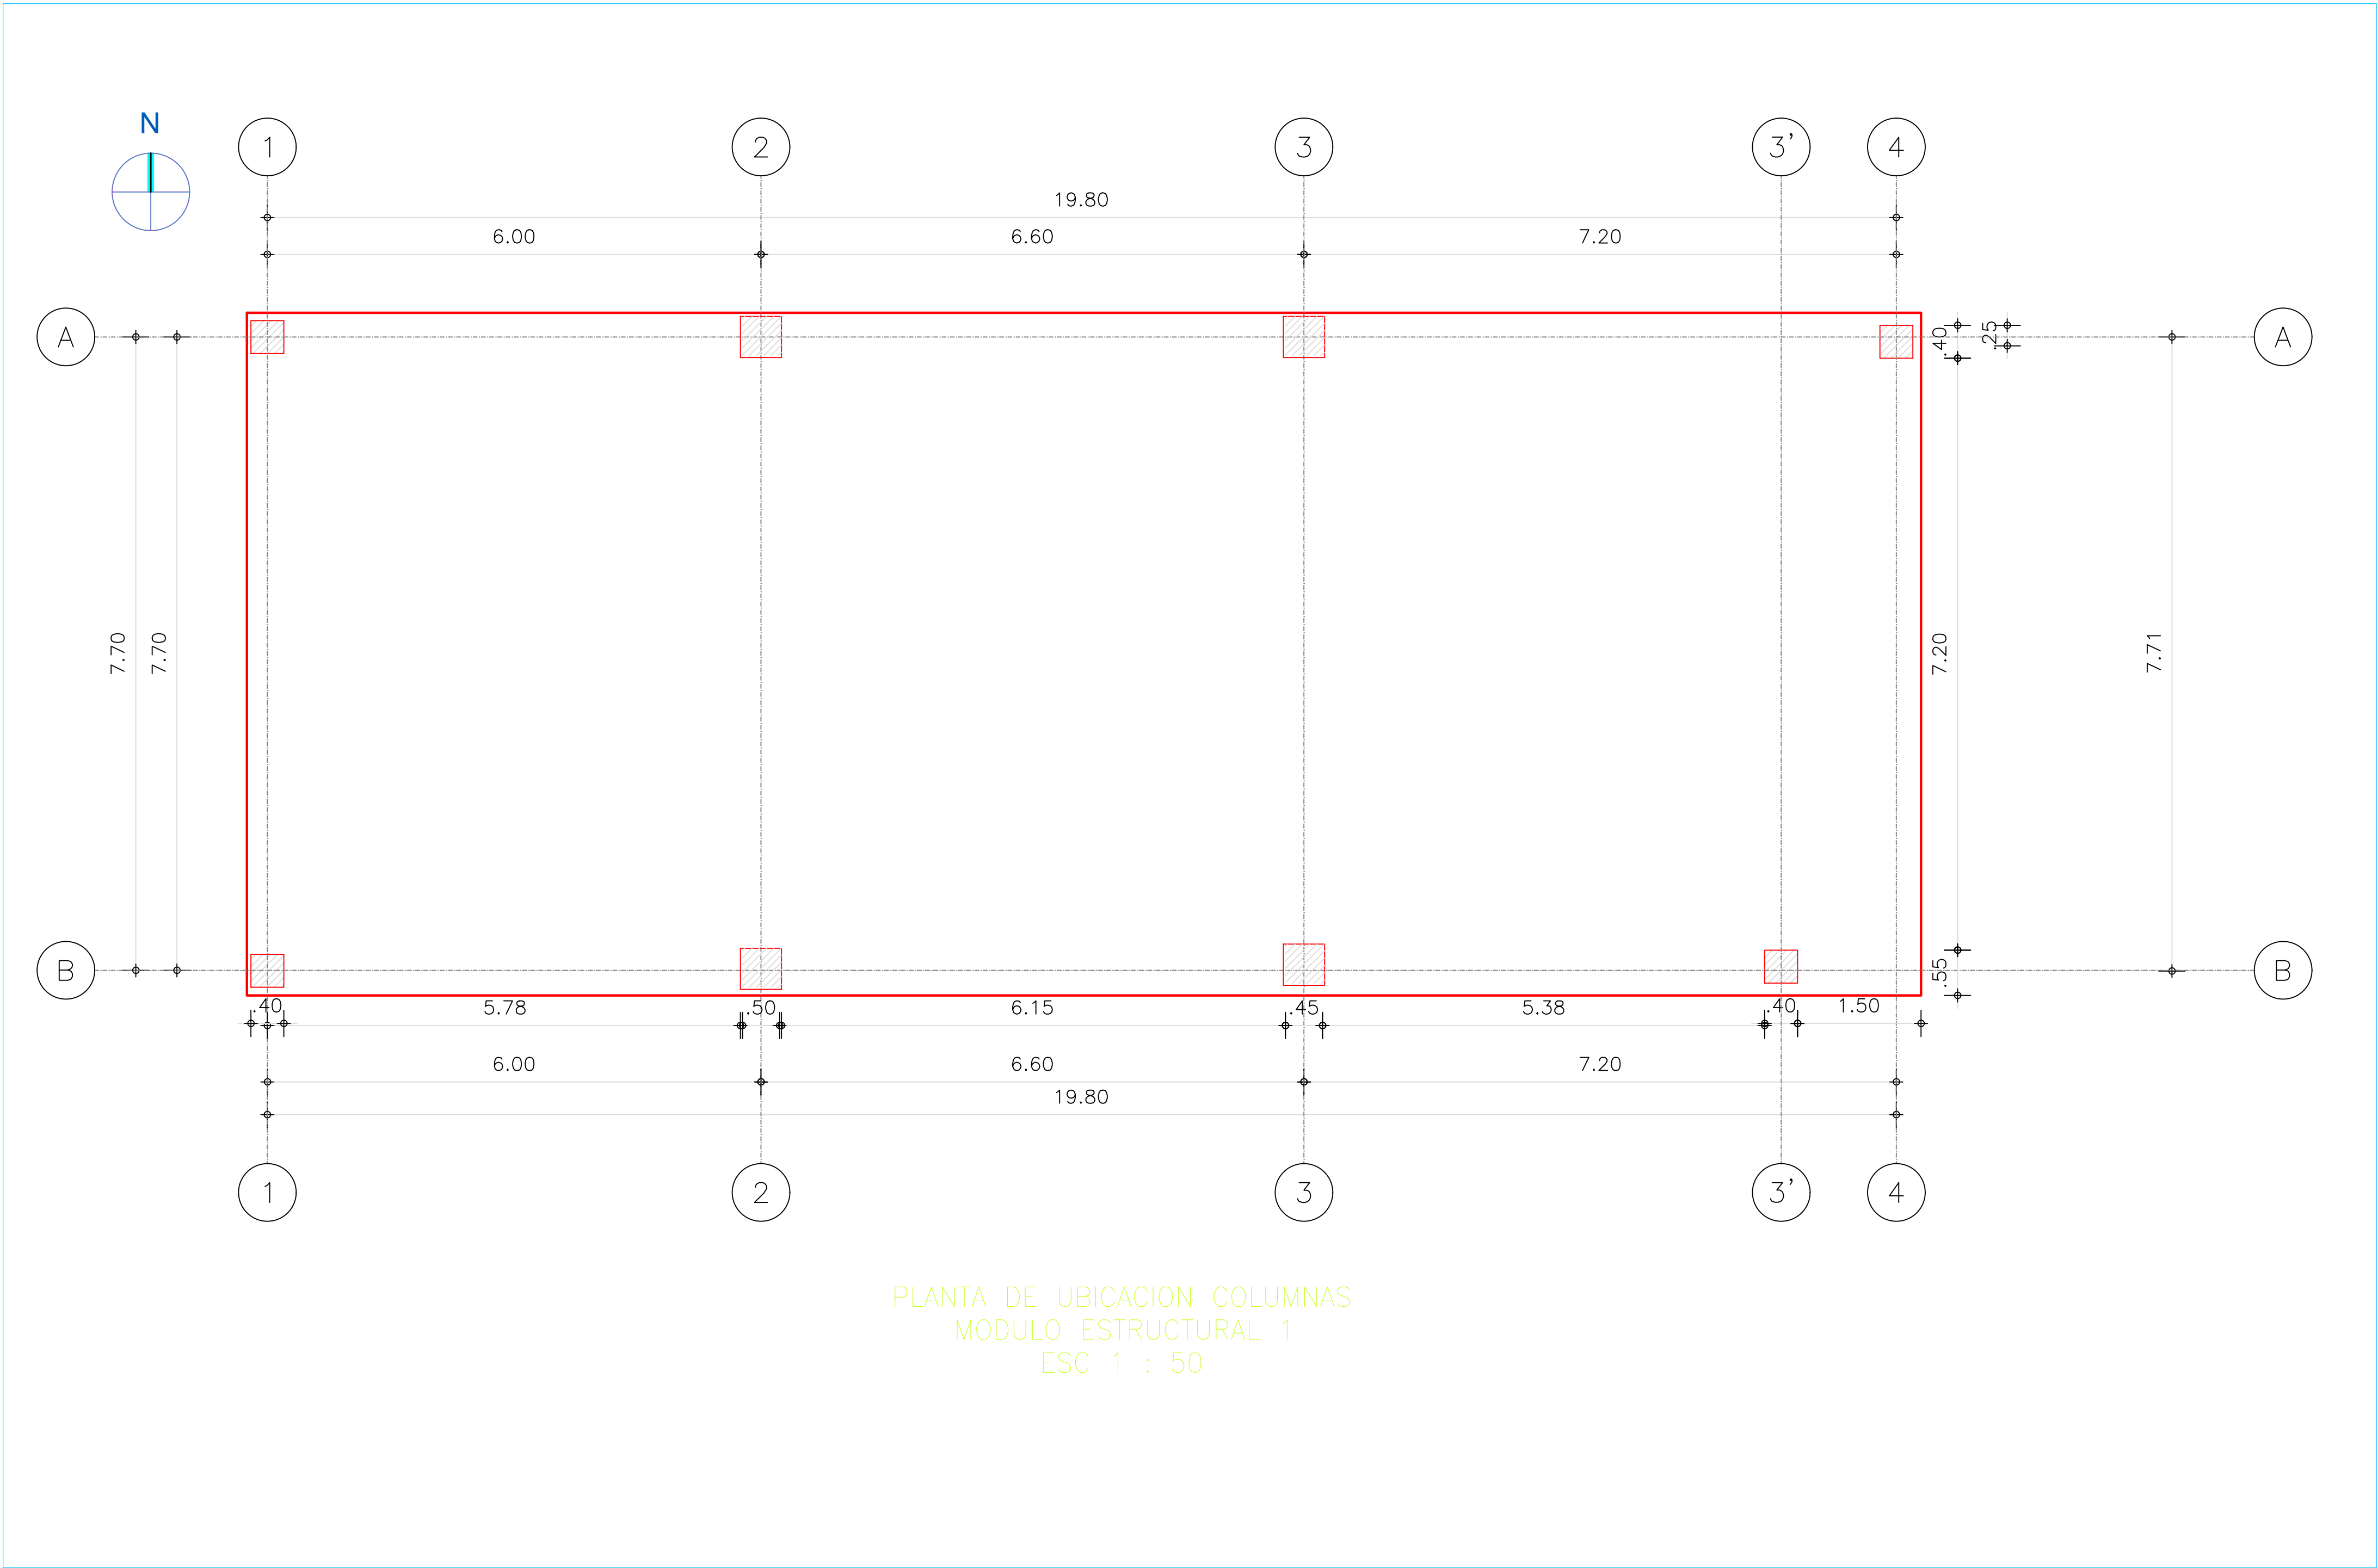


PLANTA DE UBICACION COLUMNAS
MODULO ESTRUCTURAL 1
ESC 1 : 50

UBICACIÓN MODULO 1 Esc 1:500

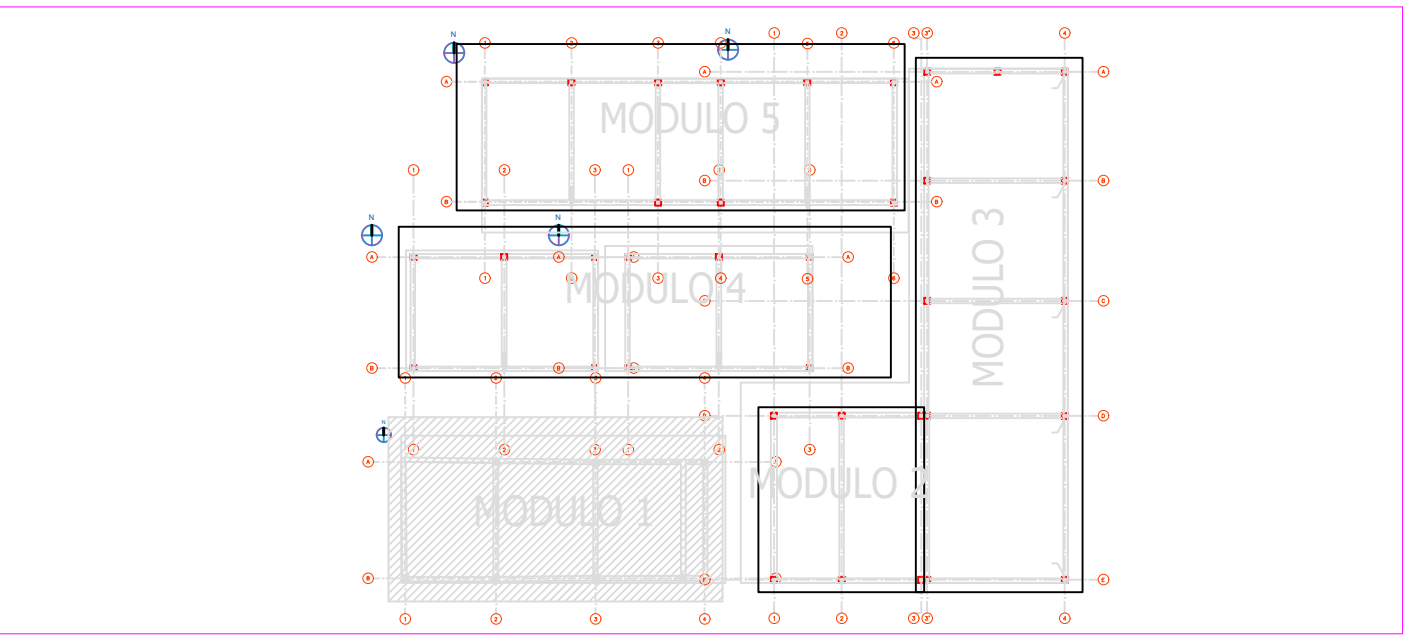

DESPIECE DE COLUMNAS –MODULO ESTRUCTURAL 1–

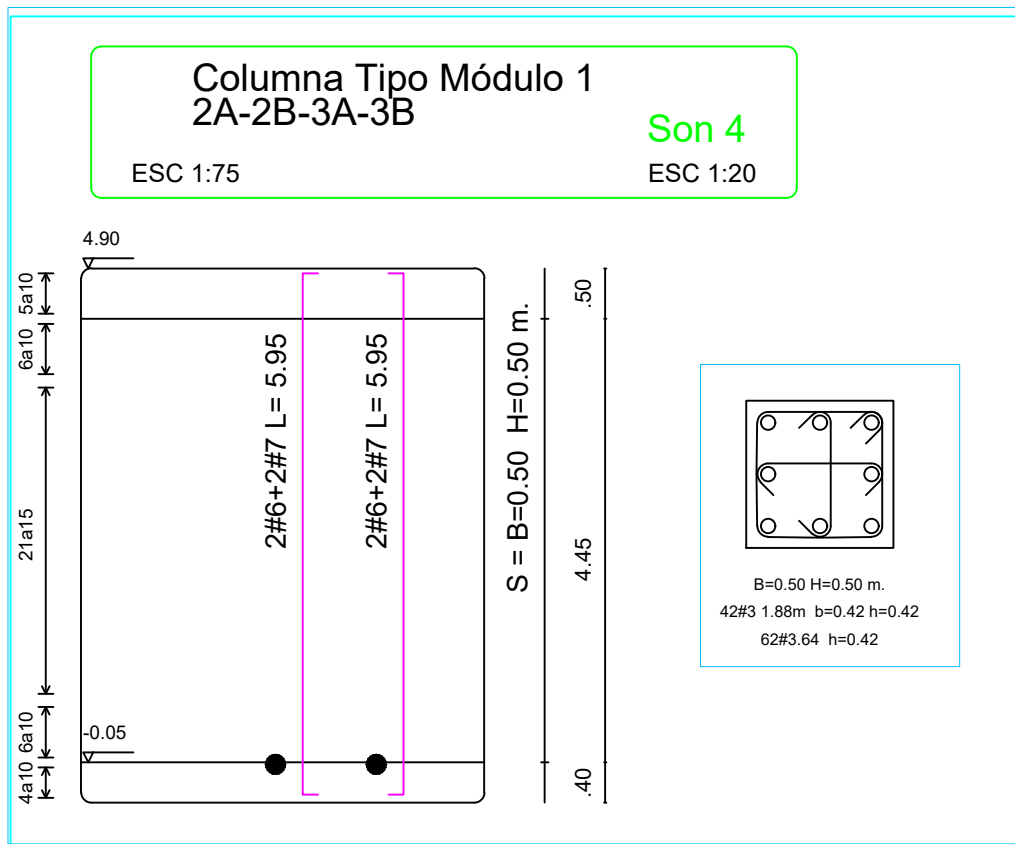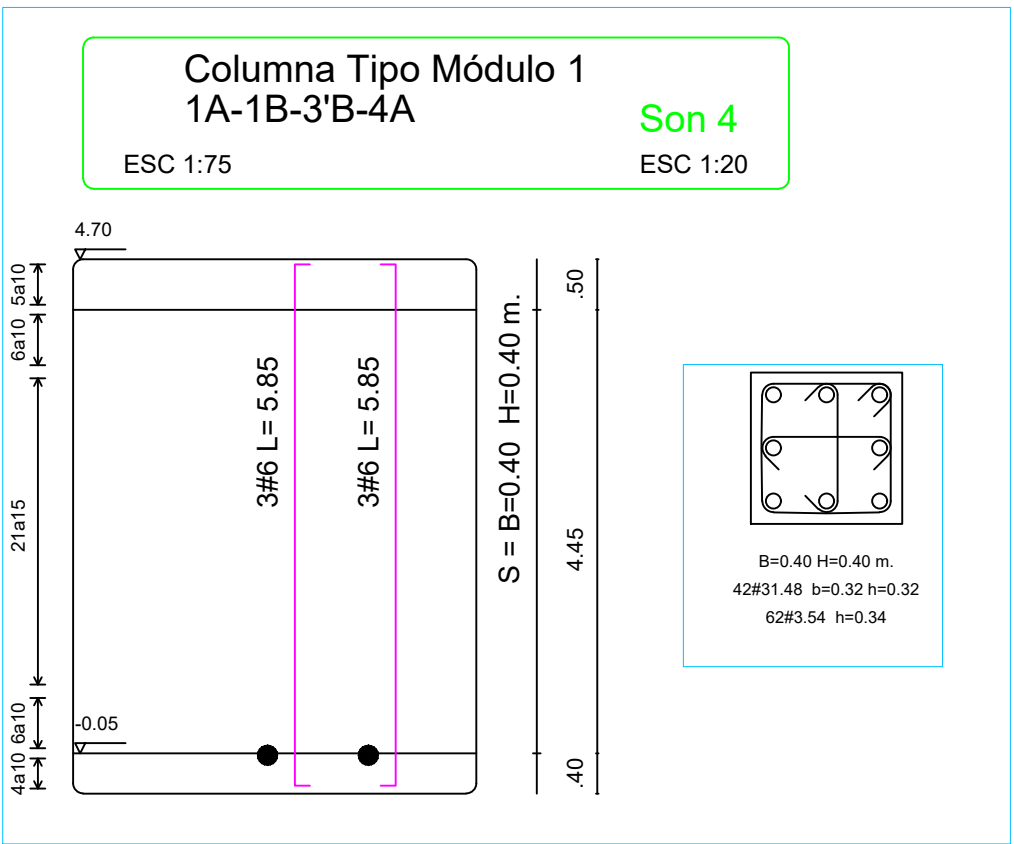

ESPECIFICACIONES TÉCNICAS

LOCALIZACION:	COEFICIENTE DE IMPORTANCIA:
NORMA DE DISEÑO: NSR-10	PERFIL DEL SUELO:
AMENAZA SISMICA: ALTA	TIPO DE CIMENTACION: Superficial (Zapata aislada)
SISTEMA DE RESISTENCIA SISMICA:	CAPACIDAD PORTANTE: 1.20 Kg/cm²
PÓRTICOS DE CONCRETO REFORZADO	PROFUNDIDAD DE CIMENTACION:
DISIPACION DE ENERGIA: ESPECIAL (DES)	MATERIALES: CONCRETO f _c = 280 Kg/cm² (4.000 PSI) ACERO DE REFUERZO Mallas electrosoldadas f _y = 4200 Kg/cm² Refuerzo varillas Ø ≥ 3/8" f _y = 4200 Kg/cm² Refuerzo varillas Ø < 3/8" f _y = 4200 Kg/cm²
VALORES:	
GRUPO DE USO:	
Grupo III — Edificaciones de atención a la comunidad	

CARGAS

CARGAS MUERTAS:	CARGAS VIVAS:
Pendientes e impermeabilización placa maciza: 0.15 tn/m²	Pendiente de la cubierta liviana inferior a 15°: 0.05 tn/m²
Cubierta liviana incluye teja y correas: 0.02 tn/m²	Carga de granizo con altitud inferior a 2000 msnm: 0.00 tn/m²

CONVENCIONES

C1 = COLUMNA DE CONFINAMIENTO
NE = Nivel Estructural
VC = Viga de Cimentación
VG = Viga
Lectura de Refuerzo en elementos Estructurales:
2#4L=4.60: Cantidad, número y longitud de la varilla
18E#3 L=90cm b=15 h=20: Cantidad, Estribo, número y longitud de la varilla, base y altura del estribo

UNIDADES DE MEDIDA

TODAS LAS UNIDADES DE MEDIDA, ESTAN EXPRESADAS EN METROS, EXCEPTO LO INDICADO EN OTRAS UNIDADES

CUADRO DE TRASLAPOS Y GANCHOS

LONGITUD MINIMA DE TRASLAPO Lt		LONGITUD MINIMA DE GANCHOS L	
DIAMETRO Ø	LONGITUD (mt)	DIAMETRO Ø	LONGITUD (mt)
2	0.40	< 3	0.15
3	0.50	4	0.20
4	0.70	5	0.25
5	0.90	6	0.30
6	1.10	7	0.35
7	1.20	8	0.40